


金山岭庭院装置项目

施工图纸

2026. 07

图纸目录

序号	图纸号	图纸名称	比例	图幅
01	建施 - A-0.0	封面	NTS	A2
02	建施 - A-0.1	图纸目录	NTS	A2
03	建施 - A-1.1	首层平面图	1:25	A2
04	建施 - A-1.2	首层平面材质/说明	1:25	A2
05	建施 - A-1.3	二层平面图	1:25	A2
06	建施 - A-1.4	二层平面材质/说明	1:25	A2
07	建施 - A-1.5	首层灯具定位图	1:25	A2
08	建施 - A-1.6	二层灯具定位图	1:25	A2
09	建施 - A-1.7	剖立面索引图	1:25	A2
10	建施 - A-2.1	剖立面大样图（一）	1:25	A2
11	建施 - A-2.2	剖立面大样图（二）	1:25	A2
12	建施 - A-2.3	剖立面大样图（三）	1:25	A2
13	建施 - A-2.4	剖立面大样图（四）	1:25	A2

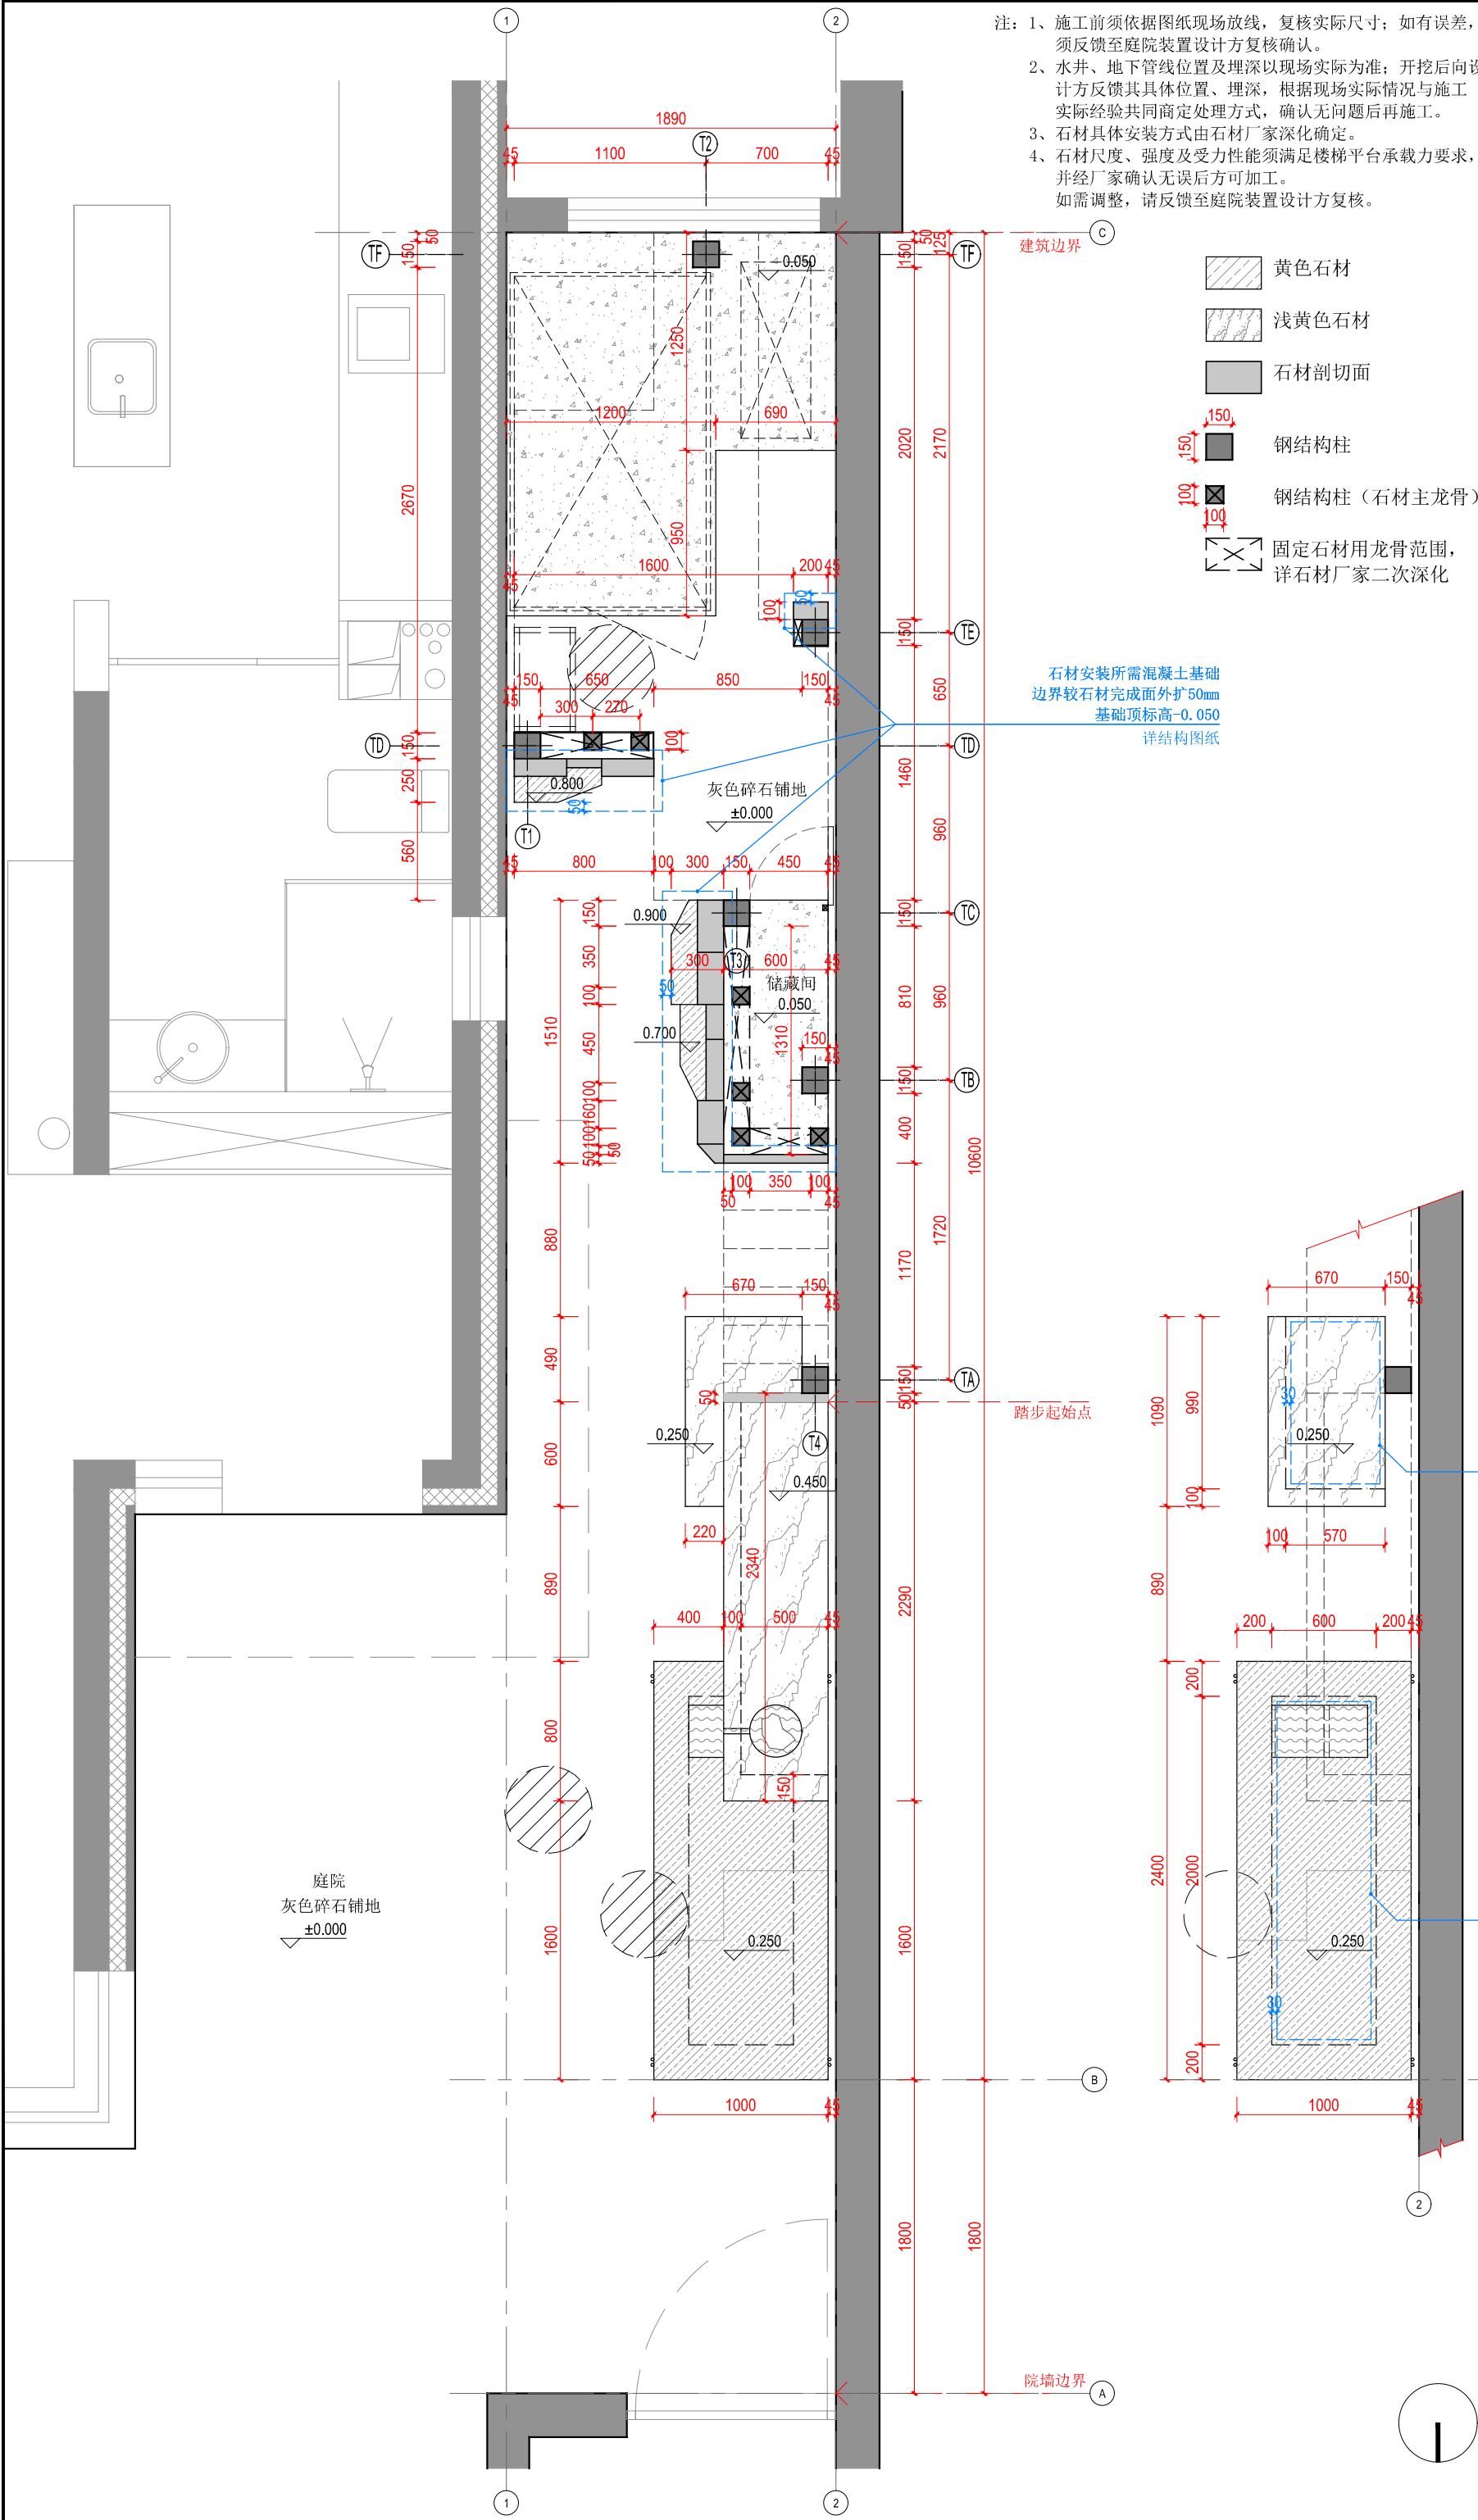

注：1、施工前须依据图纸现场放线，复核实际尺寸；如有误差，须反馈至庭院装置设计方复核确认。
2、水井、地下管线位置及埋深以现场实际为准；开挖后向设计方反馈其具体位置、埋深，根据现场实际情况与施工实际经验共同商定处理方式，确认无问题后再施工。
3、石材具体安装方式由石材厂家深化确定。
4、石材尺度、强度及受力性能须满足楼梯平台承载力要求，并经厂家确认无误后方可加工。
如需调整，请反馈至庭院装置设计方复核。

- 黄色石材
- 浅黄色石材
- 石材剖切面
- 钢结构柱
- 钢结构柱（石材主龙骨）
- 固定石材用龙骨范围，详石材厂家二次深化

石材安装所需混凝土基础
边界较石材完成面外扩50mm
基础顶标高-0.050
详结构图纸

修改版本

委托单位

项目编号

项目名称 金山岭庭院装置

项目地点 阿那亚 金山岭

审核

项目负责人

专业负责人

校对

设计

制图


图别 建施

图名 A-1.1 首层平面图

比例 A2 1:25

日期 2026年07月

首层平面图

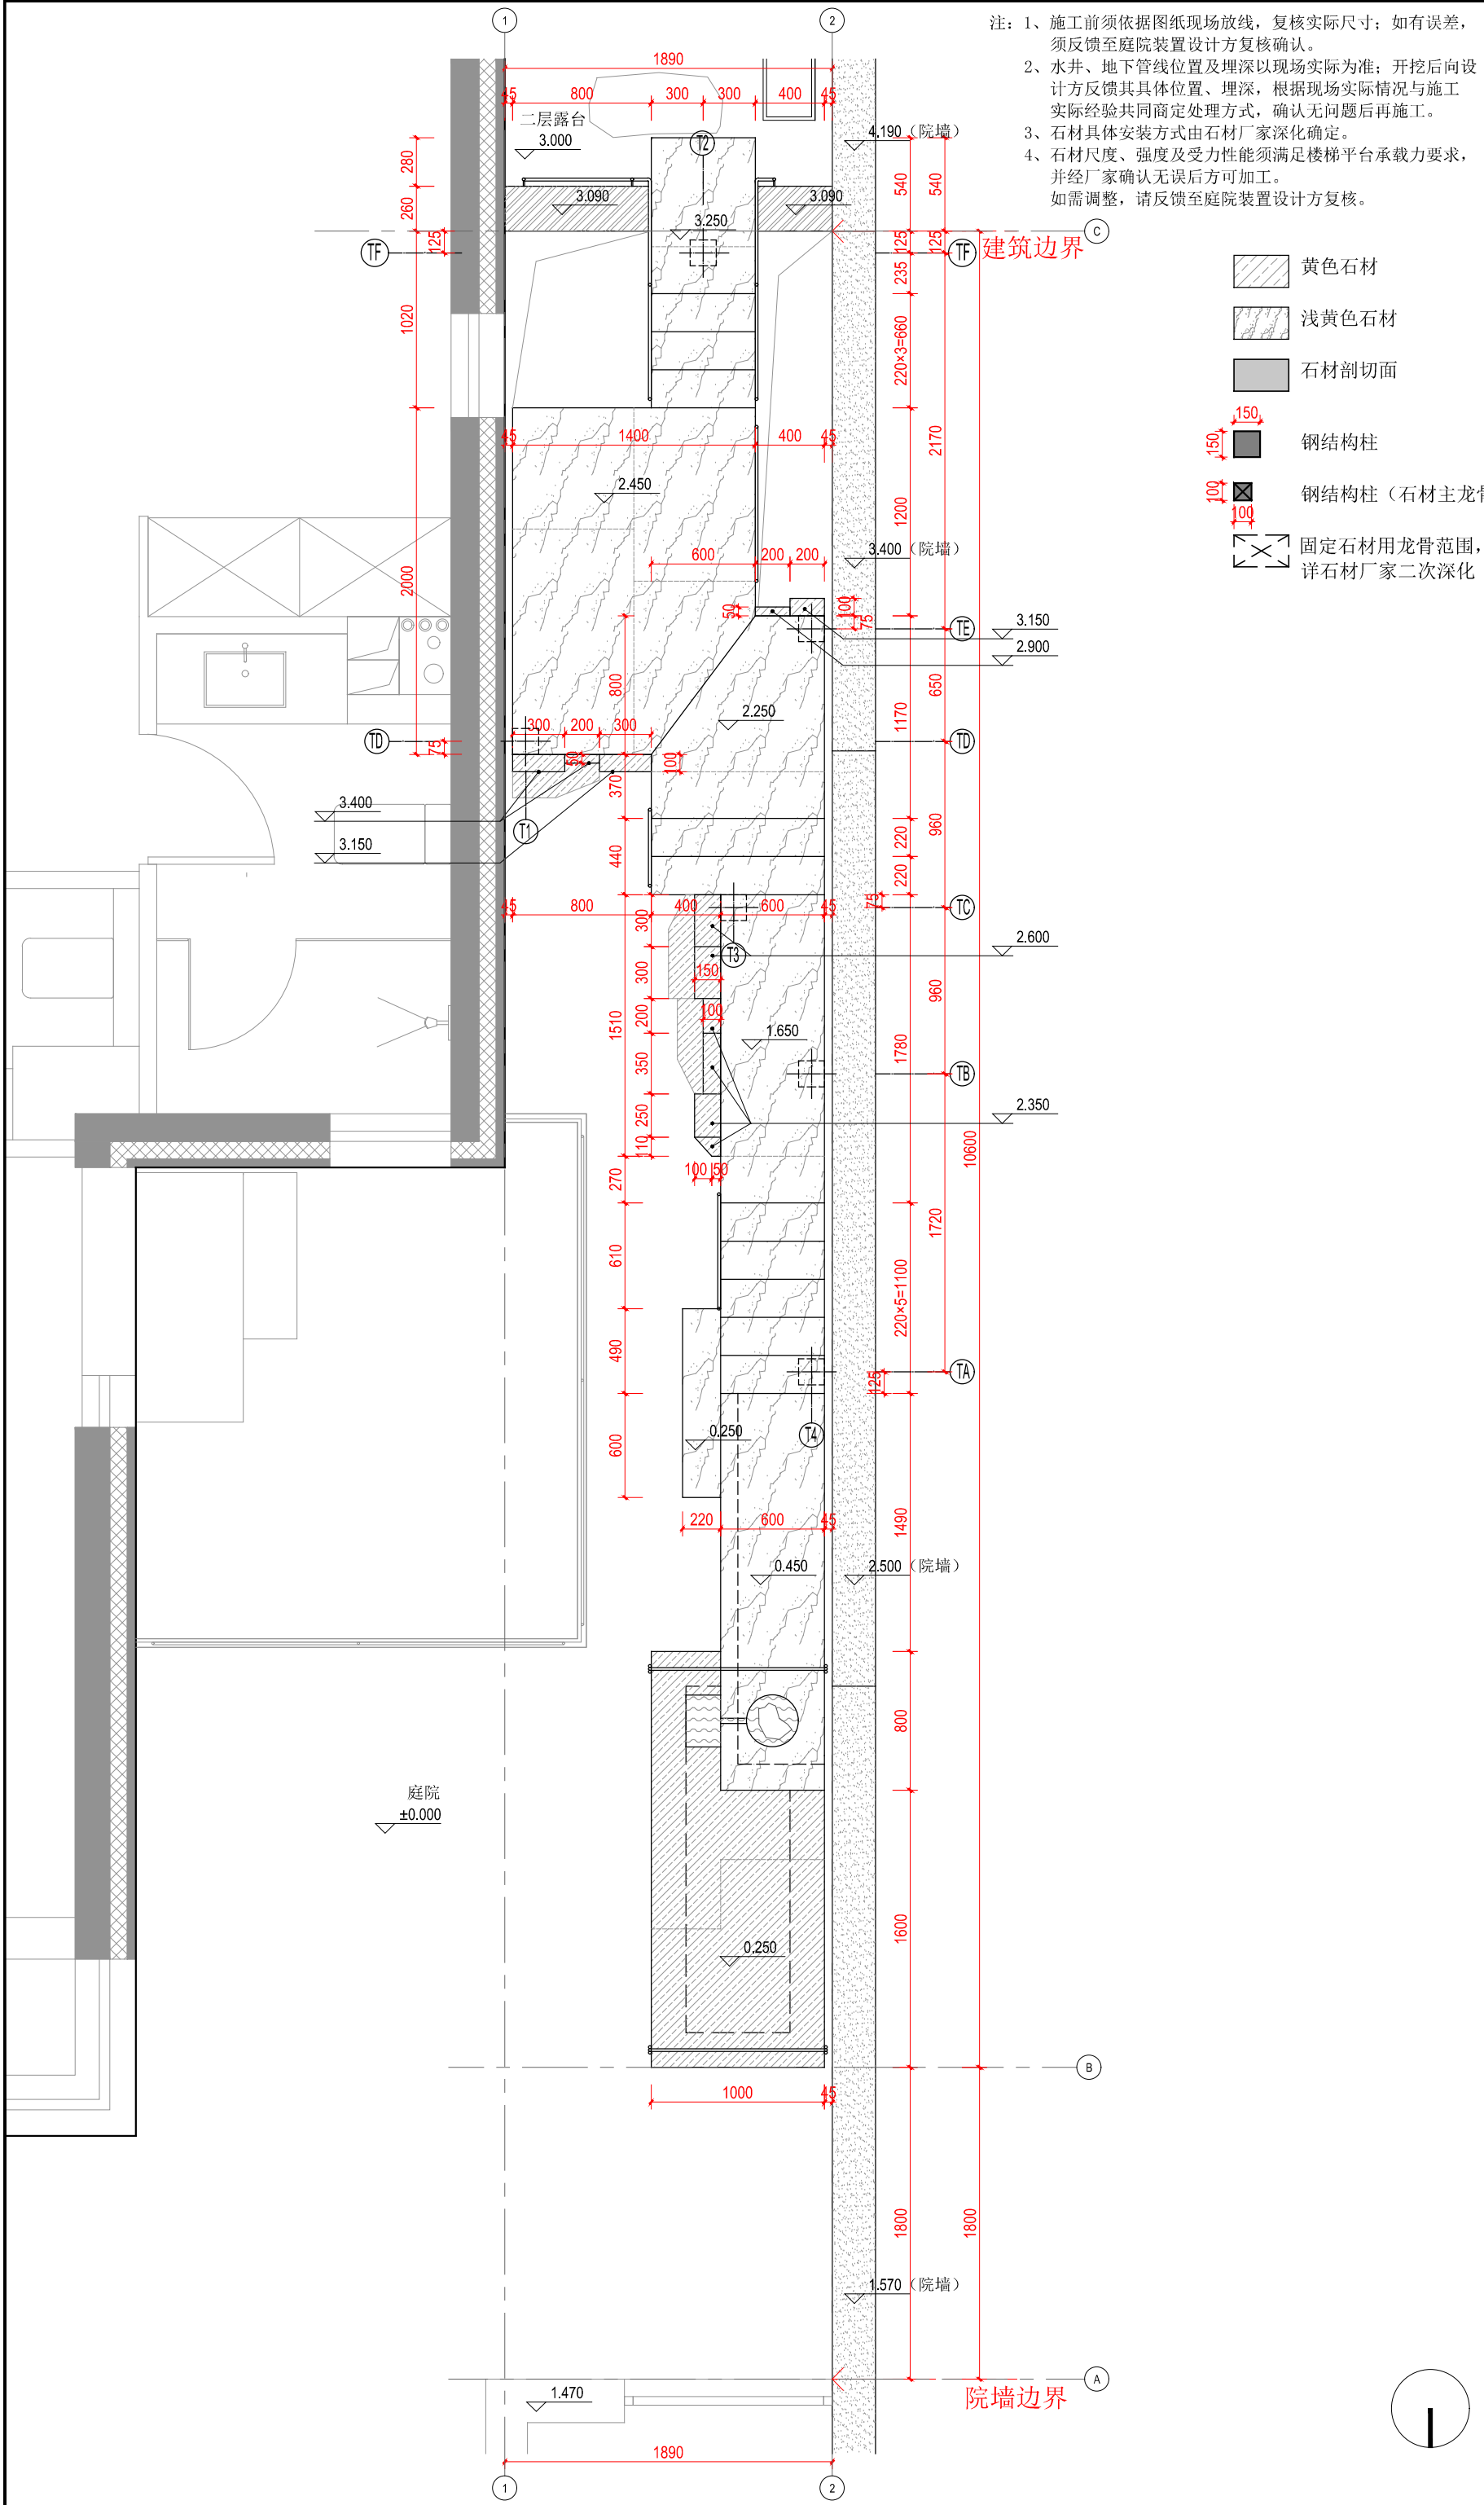

注：1、施工前须依据图纸现场放线，复核实际尺寸；如有误差，须反馈至庭院装置设计方复核确认。
2、水井、地下管线位置及埋深以现场实际为准；开挖后向设计方反馈其具体位置、埋深，根据现场实际情况与施工实际经验共同商定处理方式，确认无问题后再施工。
3、石材具体安装方式由石材厂家深化确定。
4、石材尺度、强度及受力性能须满足楼梯平台承载力要求，并经厂家确认无误后方可加工。
如需调整，请反馈至庭院装置设计方复核。

- 黄色石材
- 浅黄色石材
- 石材剖切面
- 钢结构柱
- 钢结构柱（石材主龙骨）
- 固定石材用龙骨范围，详石材厂家二次深化

修改版本

委托单位

项目编号

项目名称 金山岭庭院装置

项目地点 阿那亚 金山岭

审核

项目负责人

专业负责人

校对

设计

制图


图别 建施

图名 A-1.3 二层平面图

比例 A2 1:25

日期 2026年07月

二层平面图

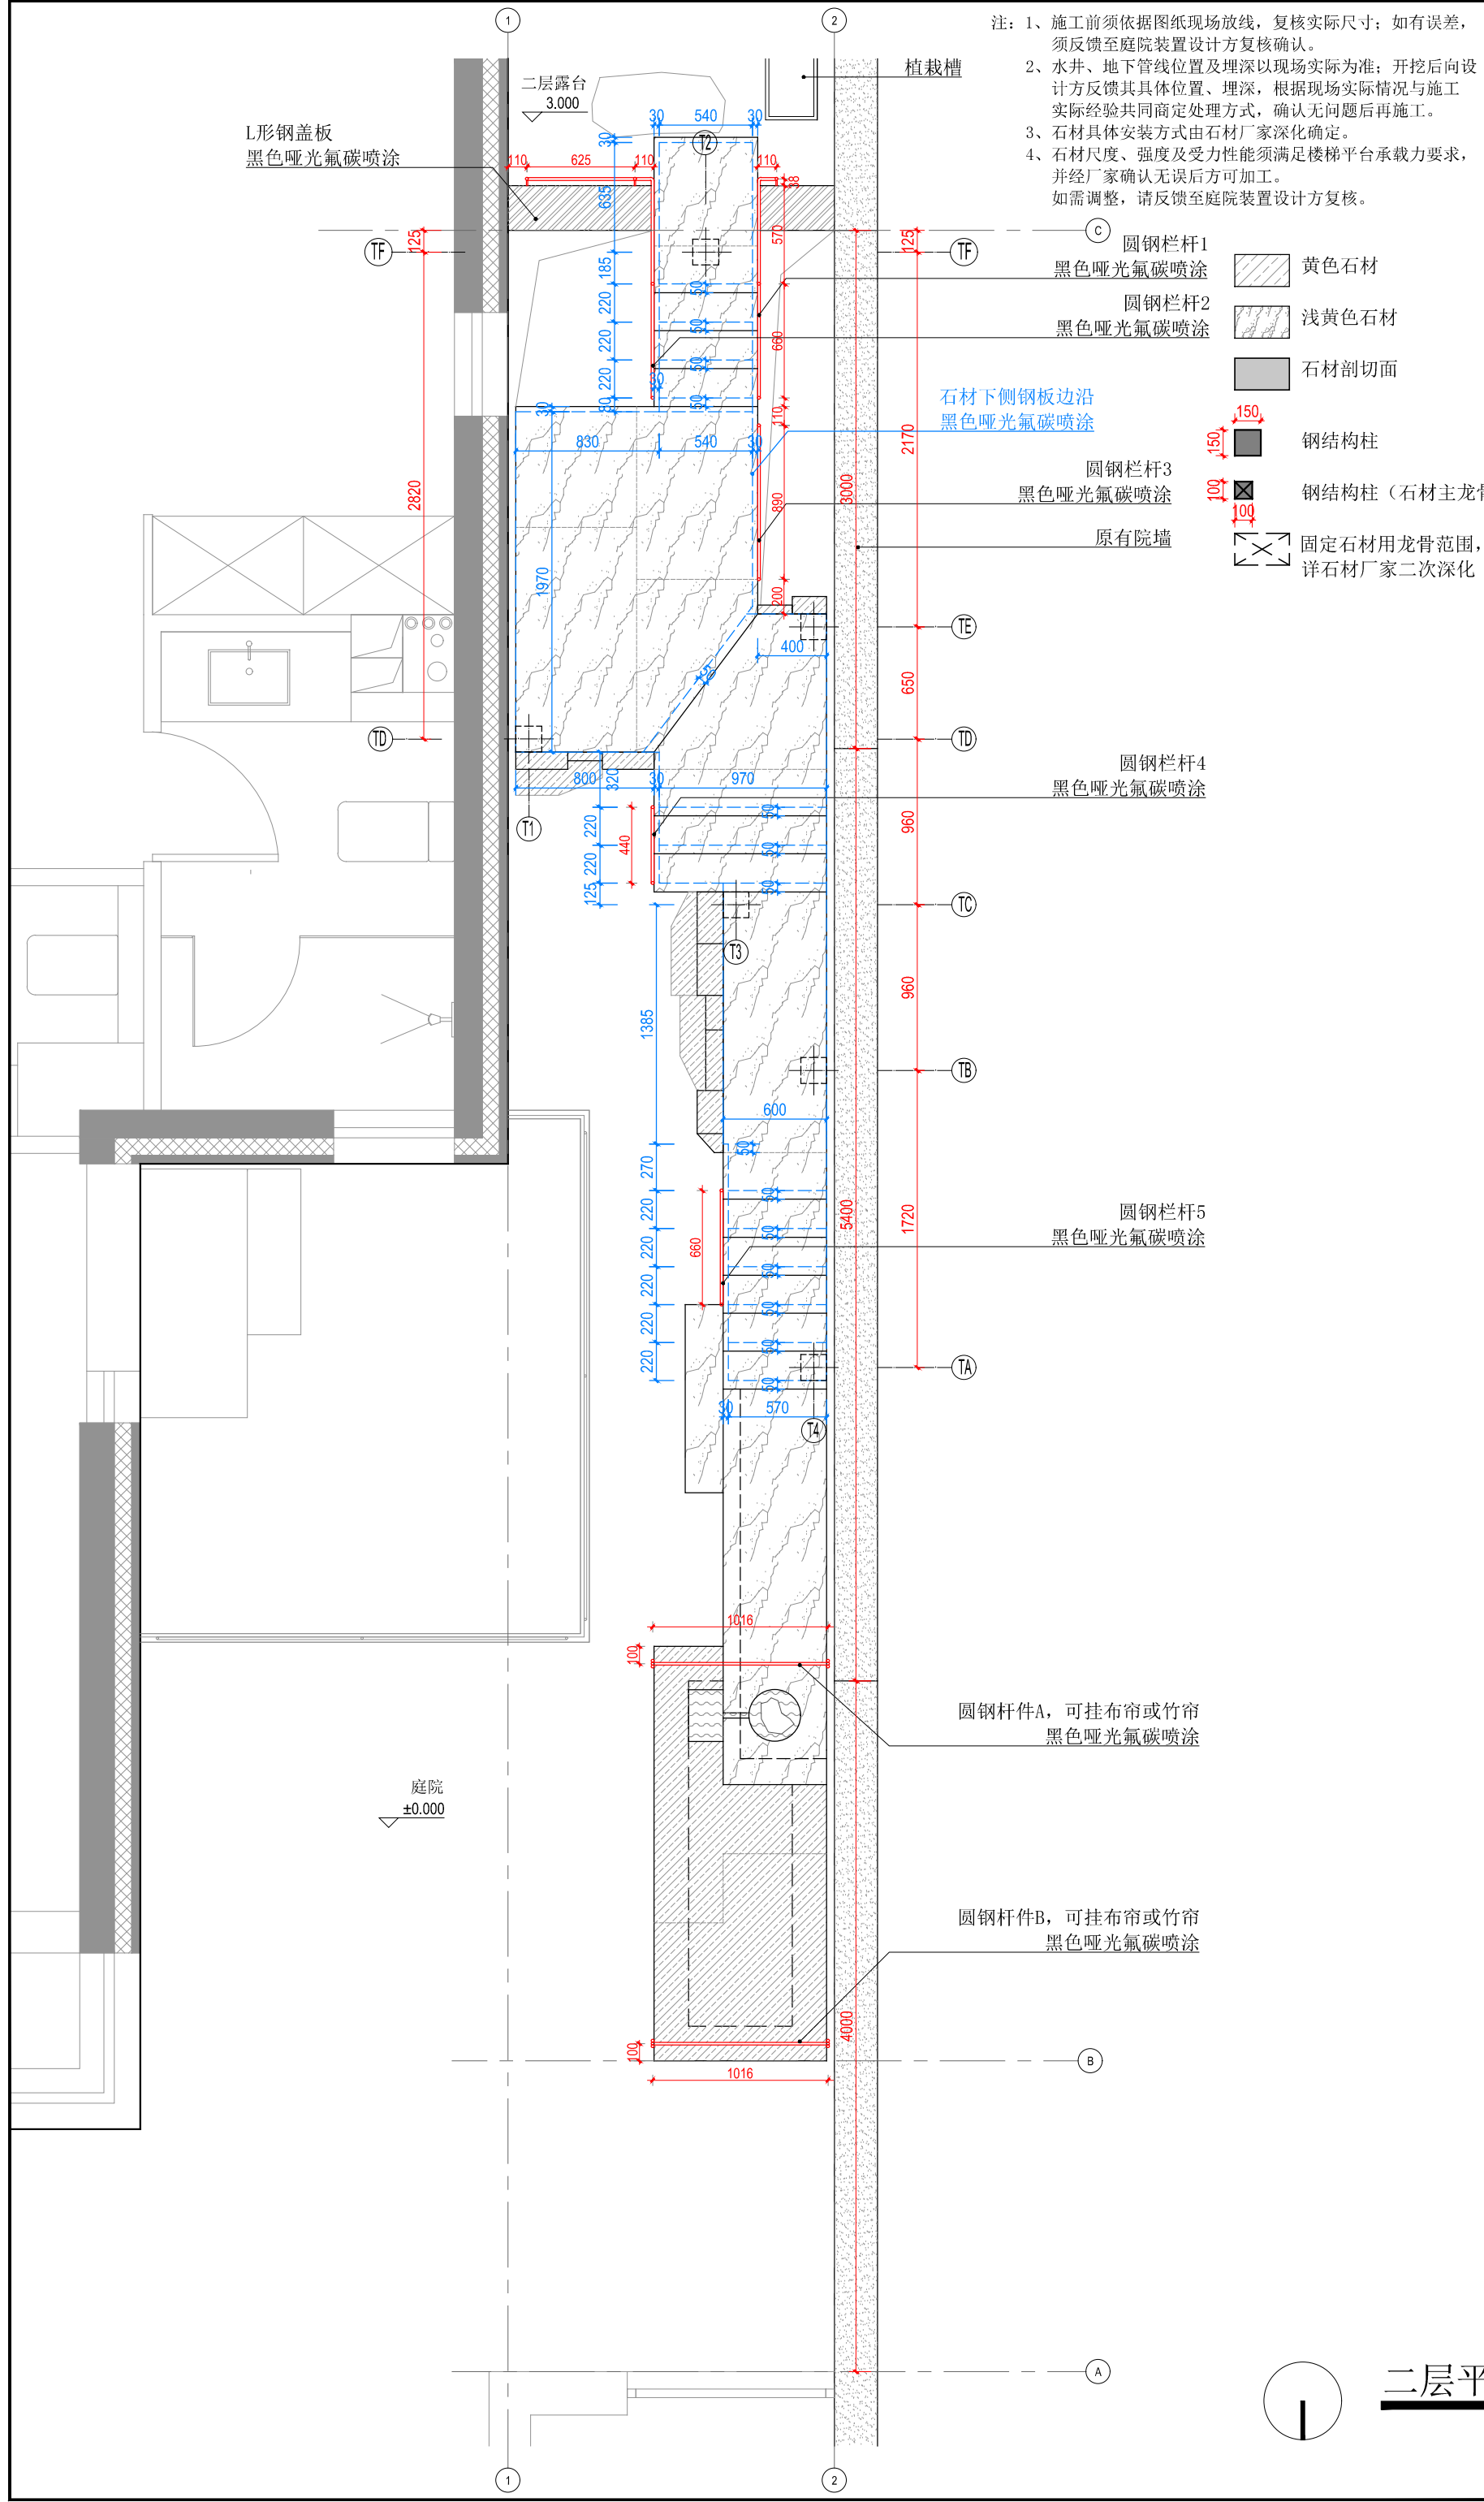

修改版本

委托单位

项目编号

项目名称

项目地点

审核

项目负责人

专业负责人

校对

设计

制图

图别 建施

图名 A-1.4 二层平面材质/说明

比例 A2 1:25

日期 2026年07月

二层平面材质/说明

注：1、施工前须依据图纸现场放线，复核实际尺寸；如有误差，须反馈至庭院装置设计方复核确认。
2、水井、地下管线位置及埋深以现场实际为准；开挖后向设计方反馈其具体位置、埋深，根据现场实际情况与施工实际经验共同商定处理方式，确认无问题后再施工。
3、石材具体安装方式由石材厂家深化确定。
4、石材尺度、强度及受力性能须满足楼梯平台承载力要求，并经厂家确认无误后方可加工。
如需调整，请反馈至庭院装置设计方复核。

修改版本

委托单位
项目编号
项目名称 金山岭庭院装置
项目地点 阿那亚 金山岭

审核

项目负责人


专业负责人

校对

设计

制图

图别 建施
图名 A-1.5 首层灯具定位图
比例 A2 1:25
日期 2026年07月

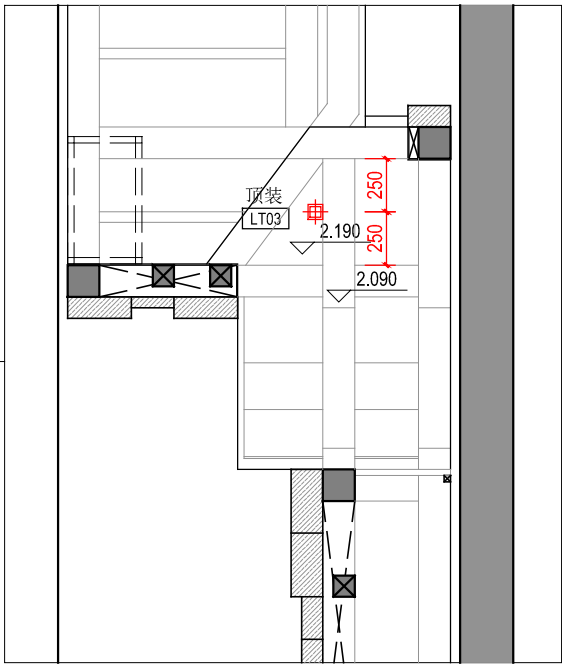



局部天花灯具定位尺寸图

- 黄色石材
- 浅黄色石材
- 石材剖切面
- 钢结构柱
- 钢结构柱 (石材主龙骨)
- 固定石材用龙骨范围，详石材厂家二次深化
- LT01 地面嵌入式防水射灯
- LT02 防水地灯 (定位及选型需结合相邻区域的景观设计，进行二次深化)
- LT03 明装防水筒灯
- 户外防水插座

注：开关的位置建议结合相邻区域景观设计统一考虑
所有户外线路应暗敷，不得外露

首层灯具定位图

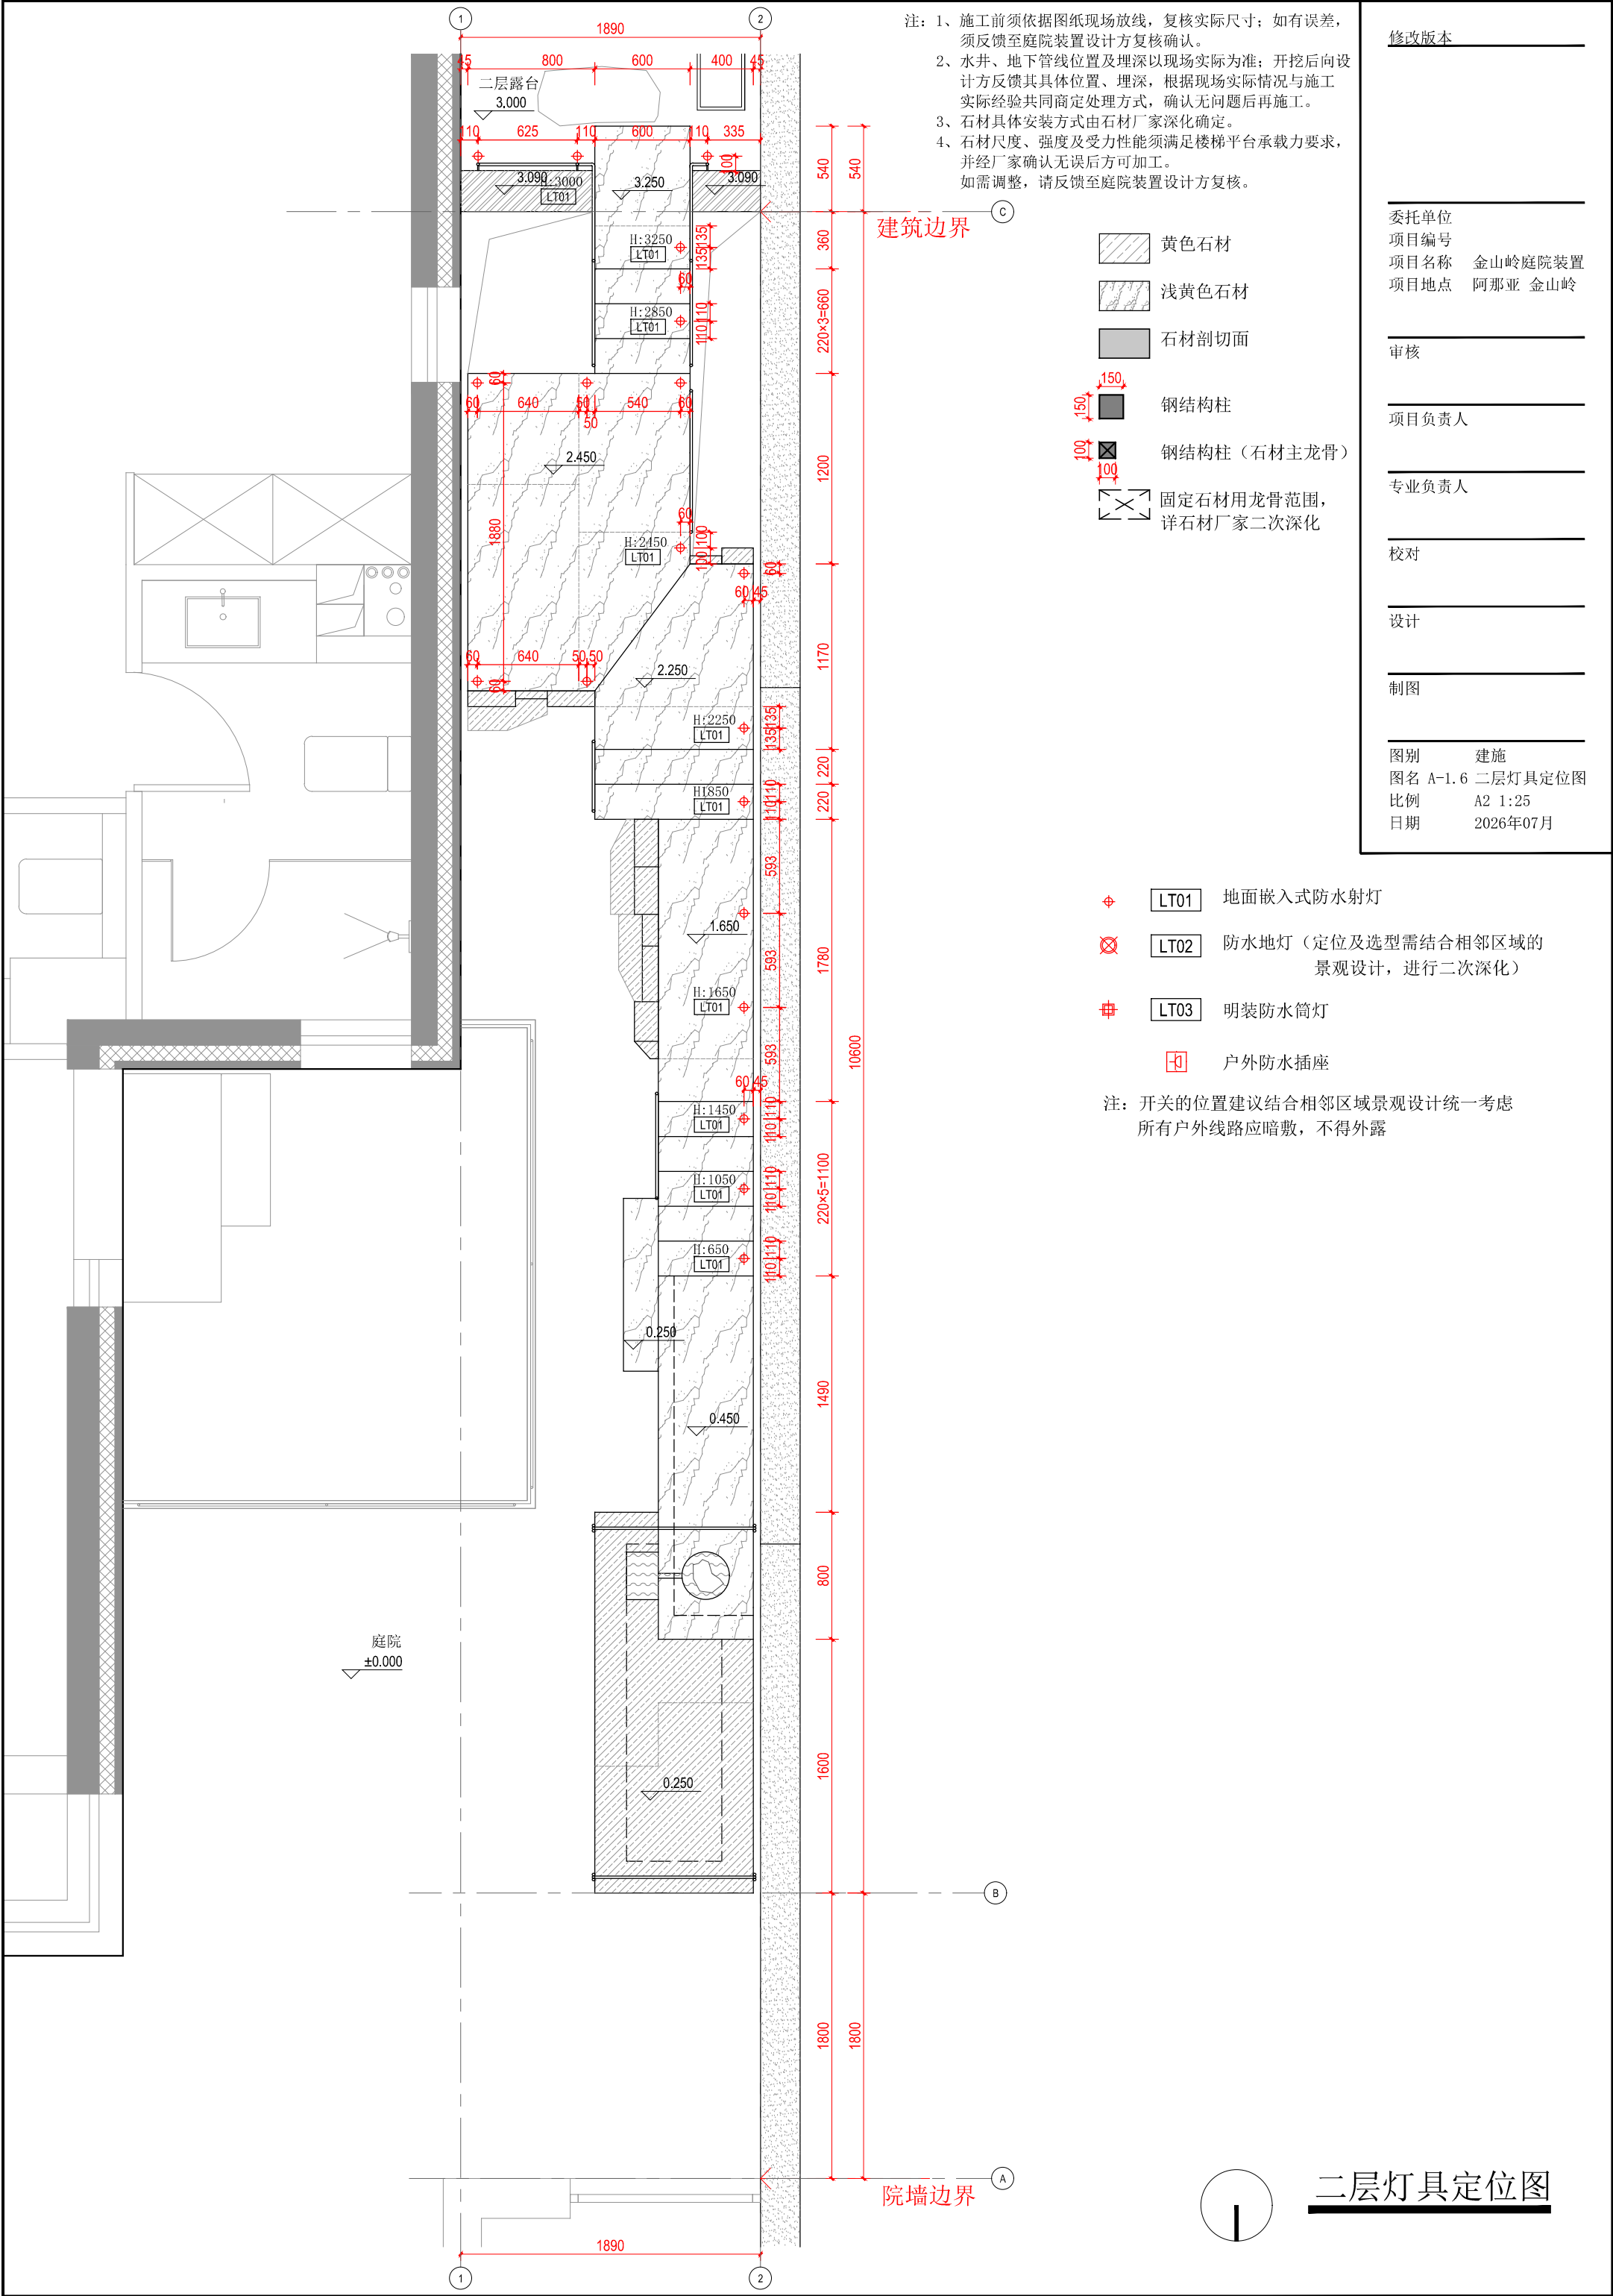

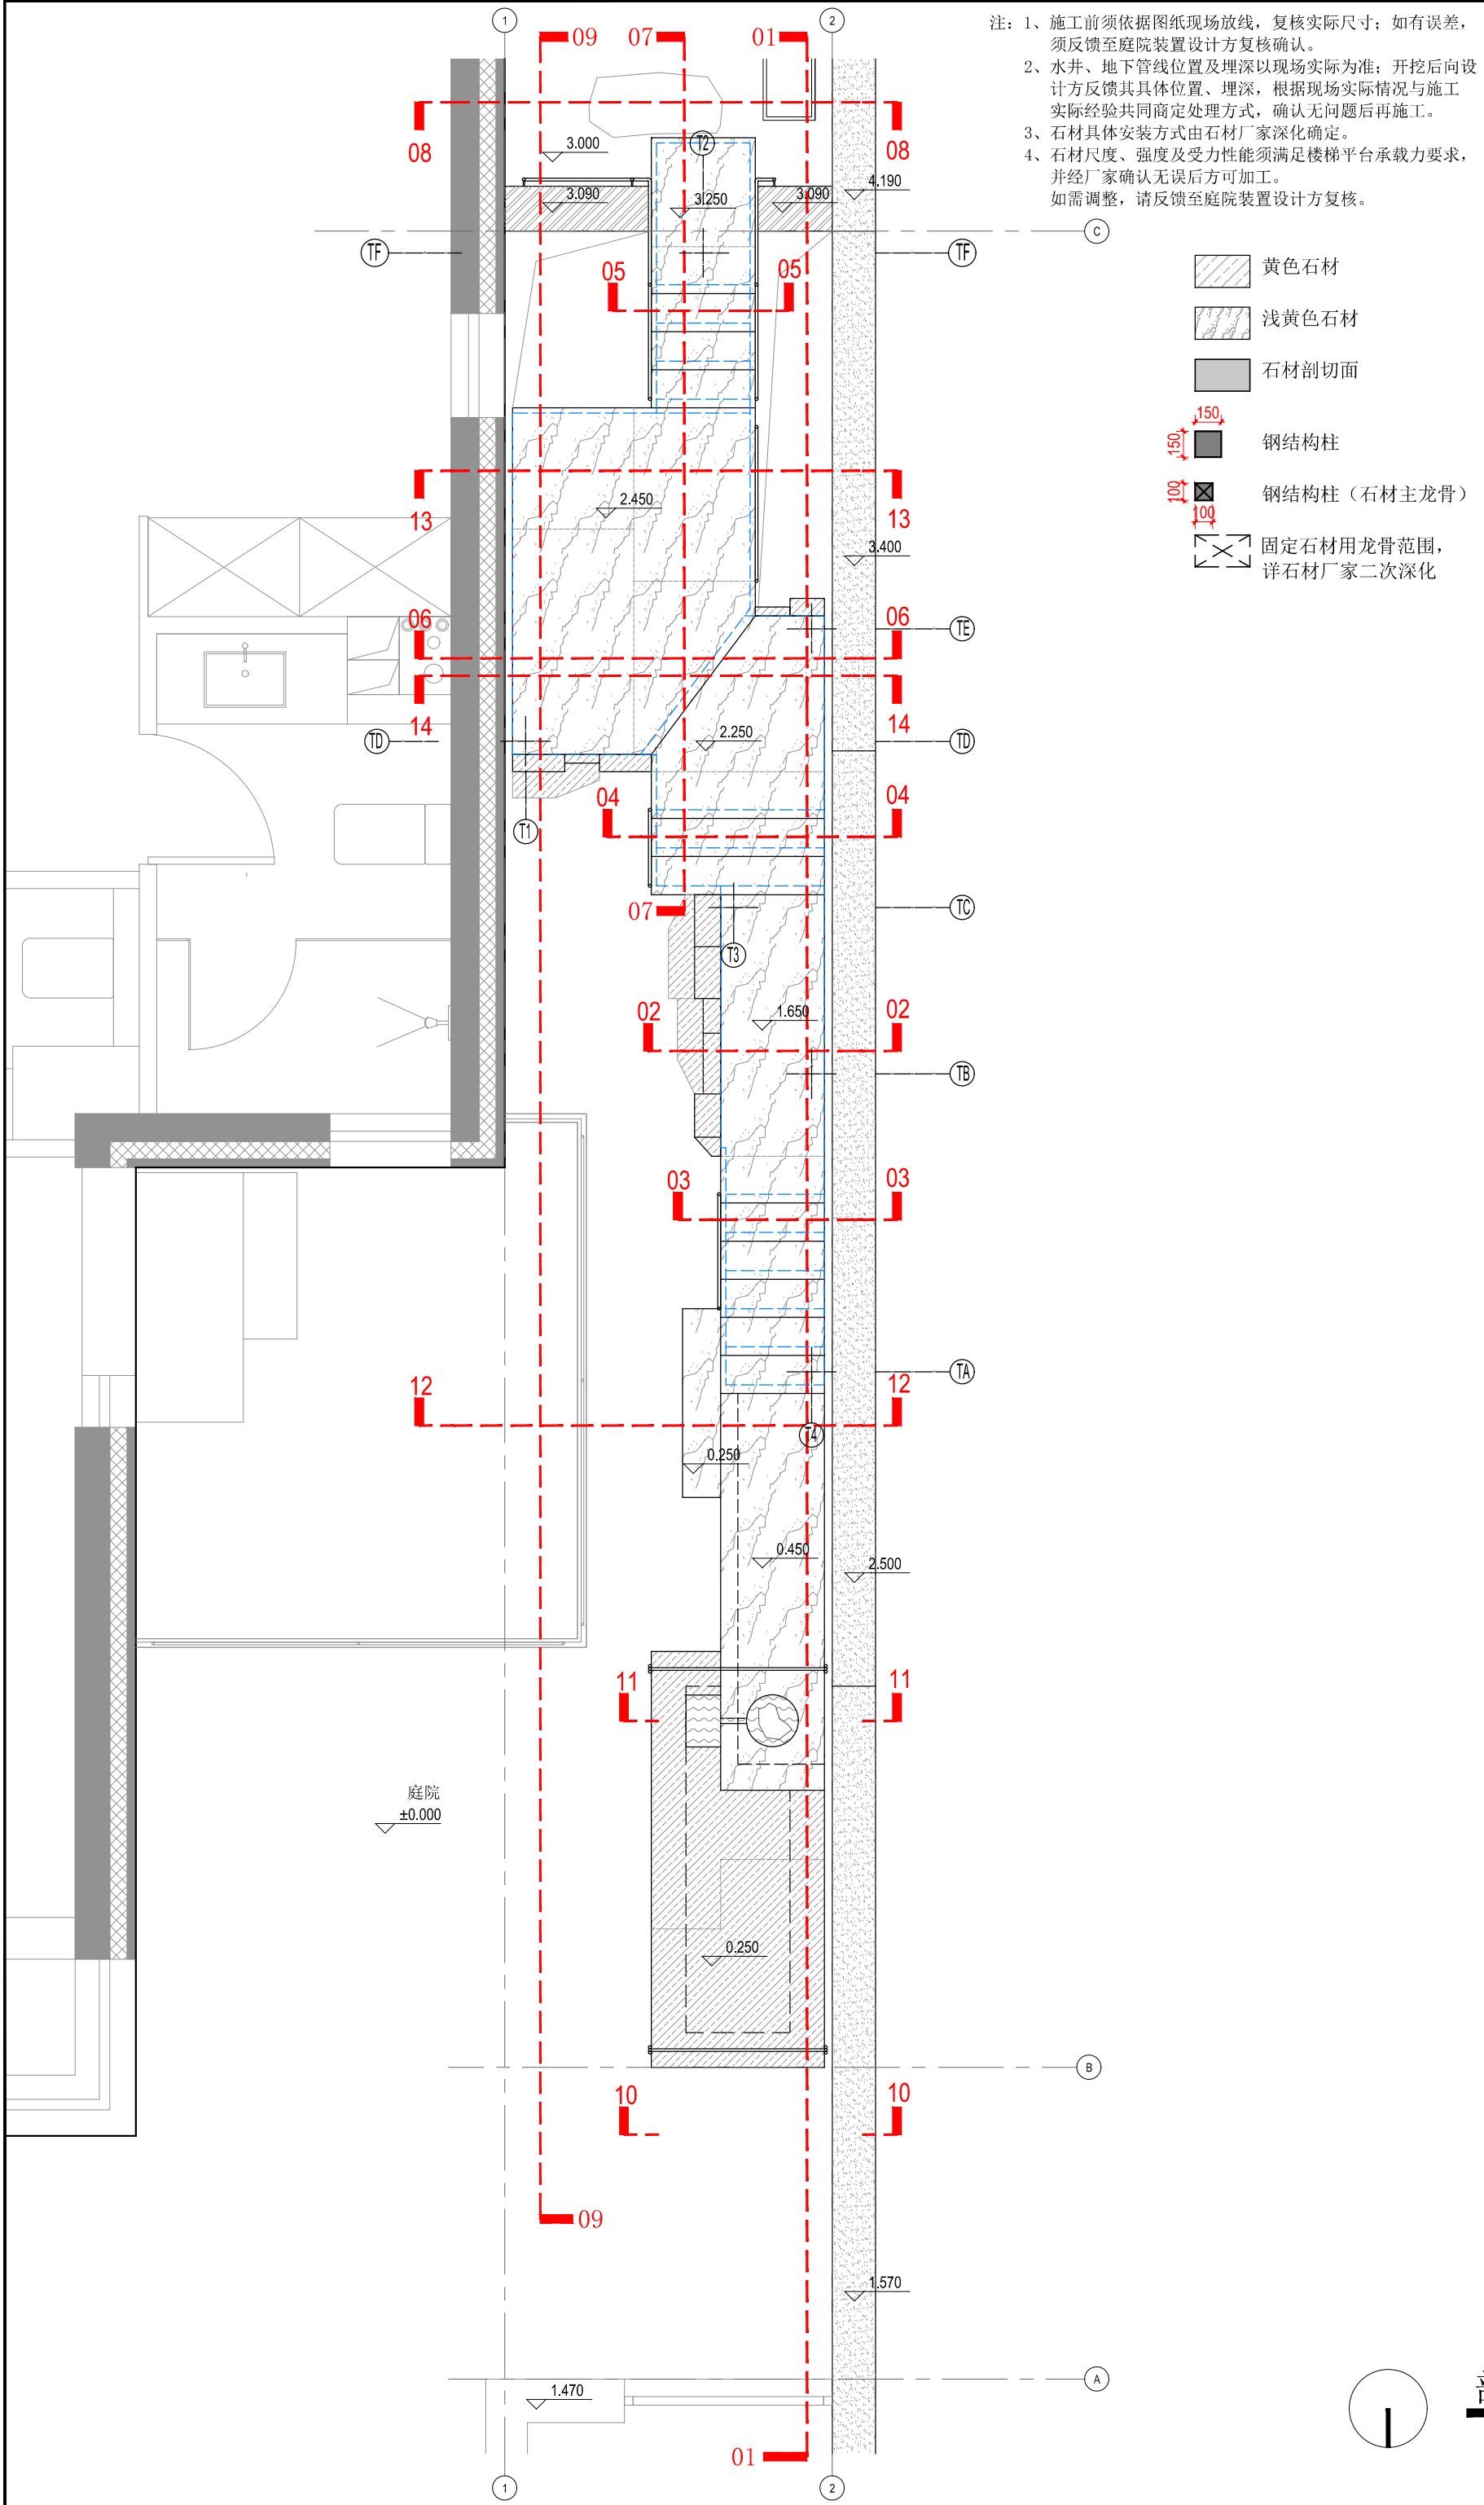

修改版本

委托单位

项目编号

项目名称 金山岭庭院装置

项目地点 阿那亚 金山岭

审核

项目负责人

专业负责人

校对

设计

制图



图别 建施

图名 A-1.7 剖立面索引图

比例 A2 1:25

日期 2026年07月

剖立面索引图

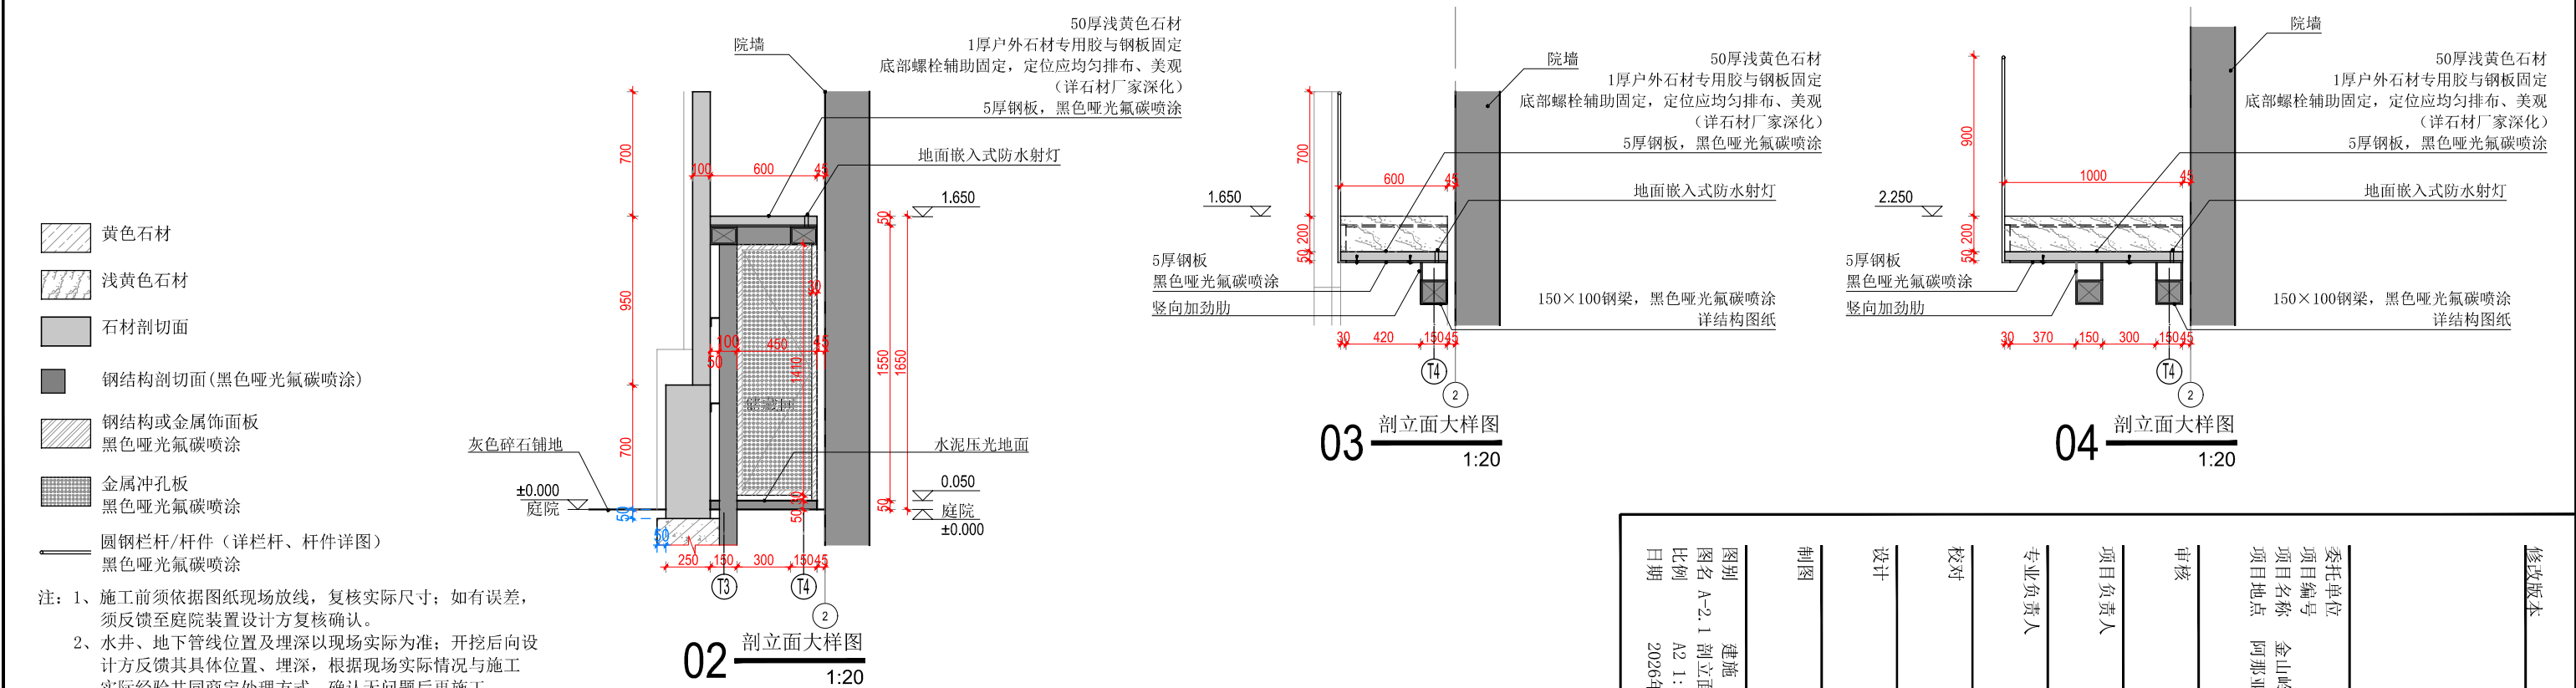
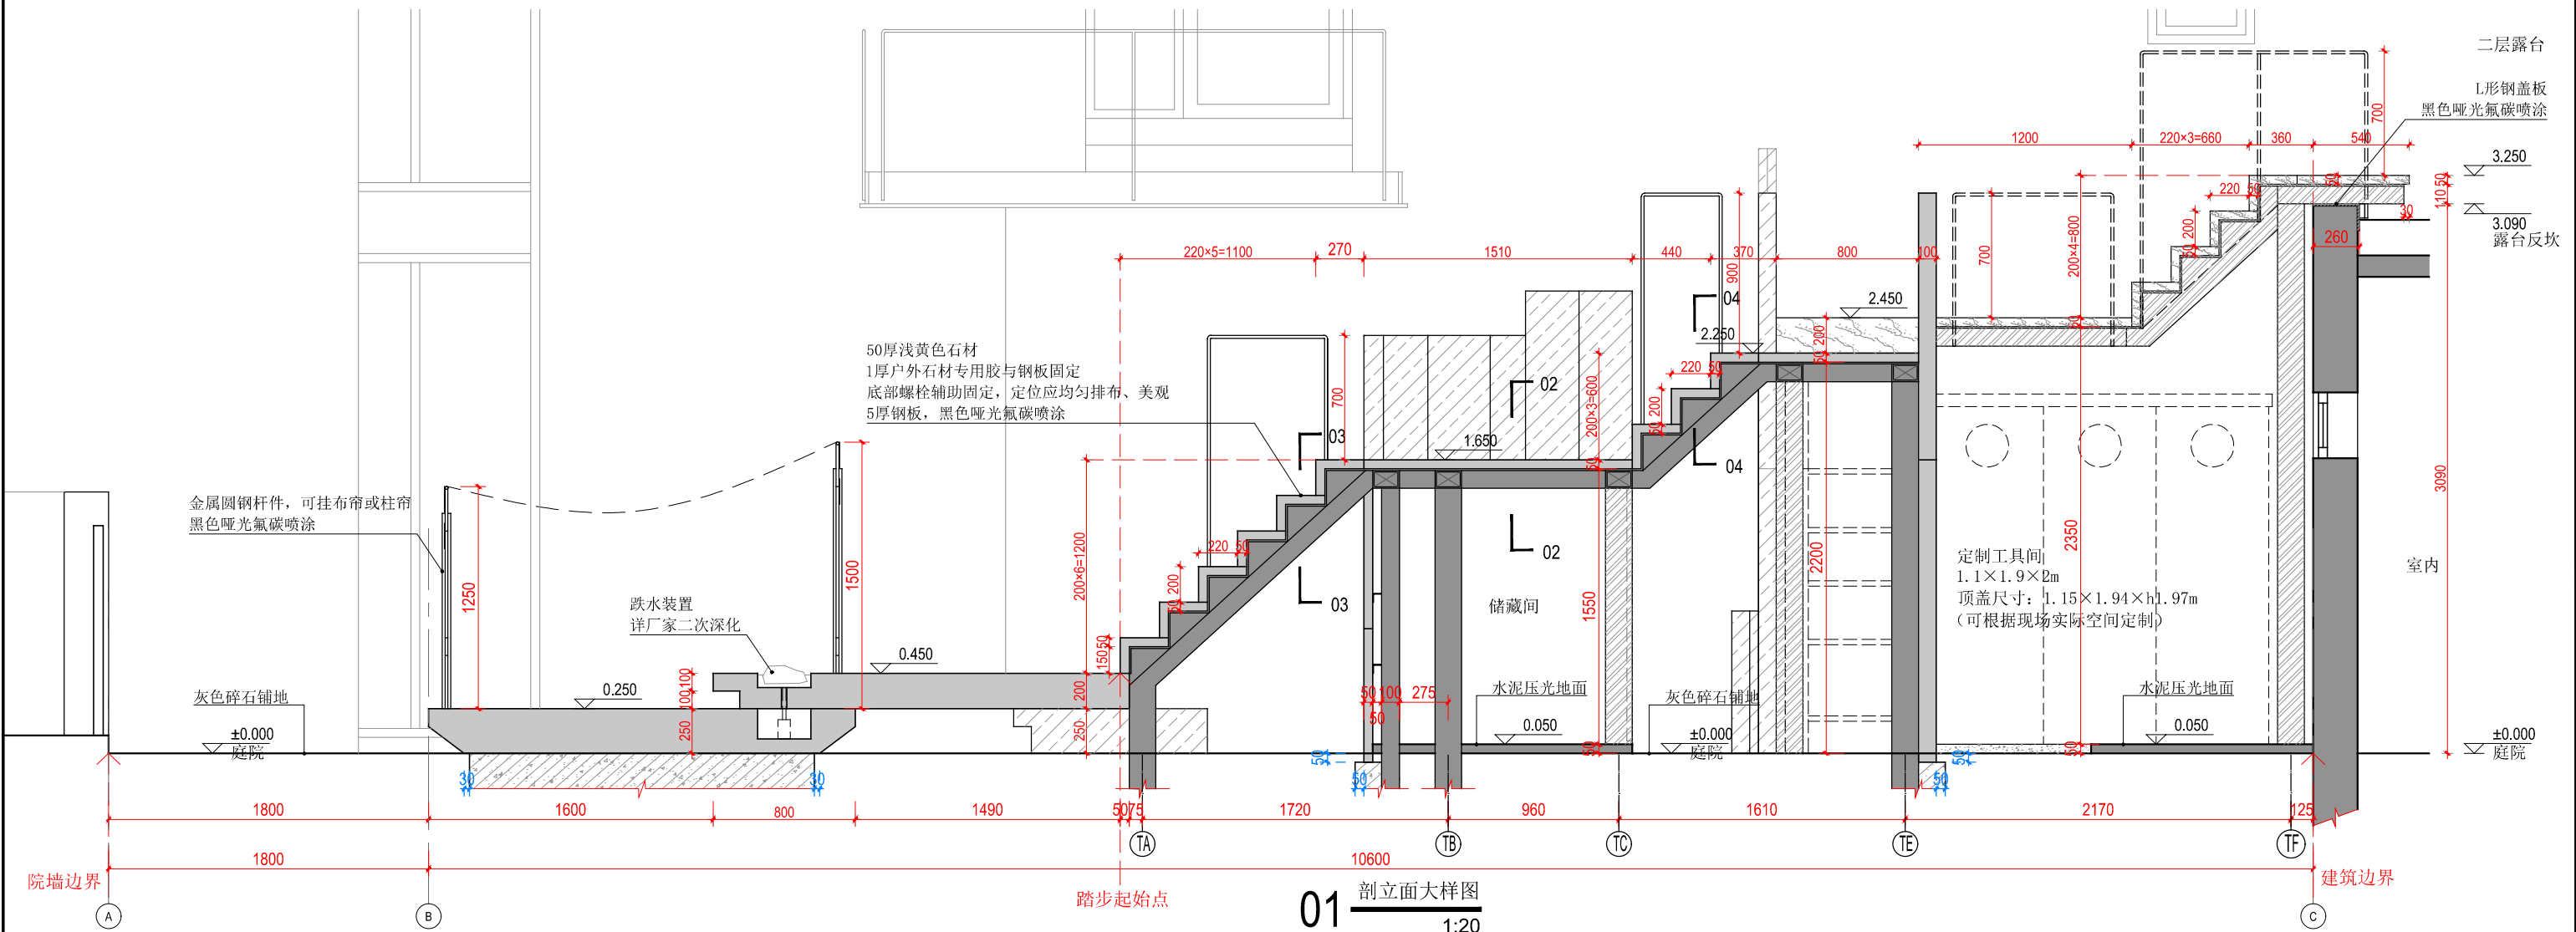


- 黄色石材
- 浅黄色石材
- 石材剖切面
- 钢结构剖切面(黑色哑光氟碳喷涂)
- 钢结构或金属饰面板
黑色哑光氟碳喷涂
- 金属冲孔板
黑色哑光氟碳喷涂
- 圆钢栏杆/杆件(详栏杆、杆件详图)
黑色哑光氟碳喷涂


注：1、施工前须依据图纸现场放线，复核实际尺寸；如有误差，须反馈至庭院装置设计方复核确认。
2、水井、地下管线位置及埋深以现场实际为准；开挖后向设计方反馈其具体位置、埋深，根据现场实际情况与施工实际经验共同商定处理方式，确认无问题后再施工。
3、石材具体安装方式由石材厂家深化确定。
4、石材尺度、强度及受力性能须满足楼梯平台承载力要求，并经厂家确认无误后方可加工。
如需调整，请反馈至庭院装置设计方复核。

修改版本	
委托单位	金山岭庭院装置
项目编号	阿那亚·金山岭
项目名称	
项目地点	
审核	
项目负责	
专业负责	
校对	
设计	
制图	
图别	建施
图名	A-2.1 剖立面大样图(一)
比例	A2 1:25
日期	2026年07月

- 注：1、施工前须依据图纸现场放线，复核实际尺寸；如有误差，须反馈至庭院装置设计方复核确认。
- 2、水井、地下管线位置及埋深以现场实际为准；开挖后向设计方反馈其具体位置、埋深，根据现场实际情况与施工实际经验共同商定处理方式，确认无问题后再施工。
- 3、石材具体安装方式由石材厂家深化确定。
- 4、石材尺度、强度及受力性能须满足楼梯平台承载力要求，并经厂家确认无误后方可加工。
- 如需调整，请反馈至庭院装置设计方复核。

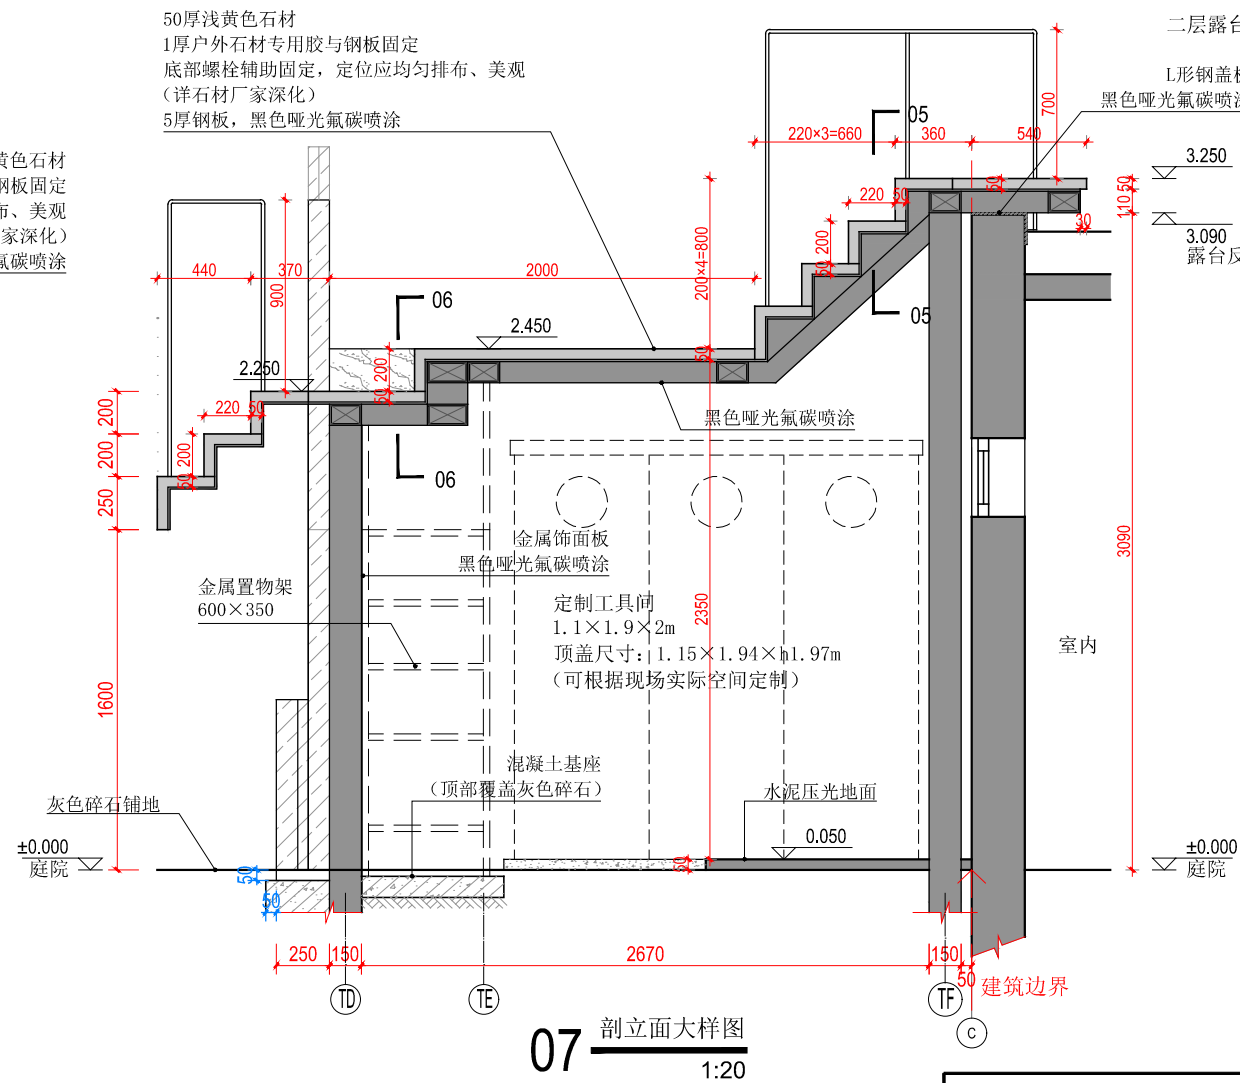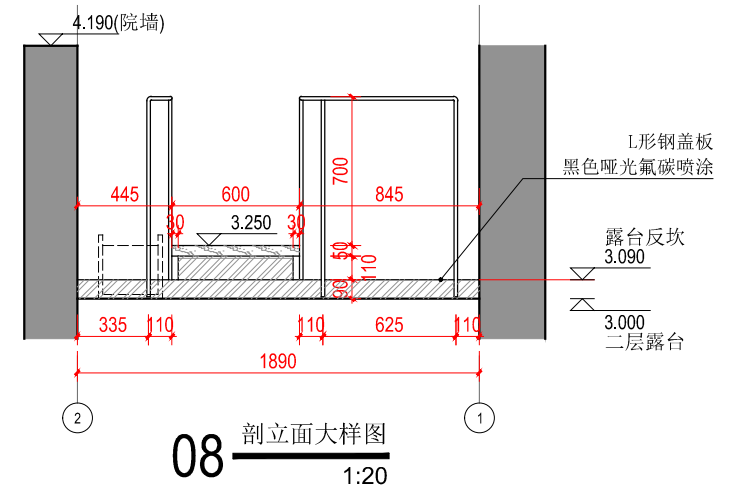


修改版本	
委托单位	
项目编号	金山岭庭院装置
项目名称	阿那亚 金山岭
项目地点	
审核	
项目负责人	
专业负责人	
校对	
设计	
制图	
图例	建施
图名	A-2.1 剖立面大样图(二)
比例	A2 1:25
日期	2026年07月

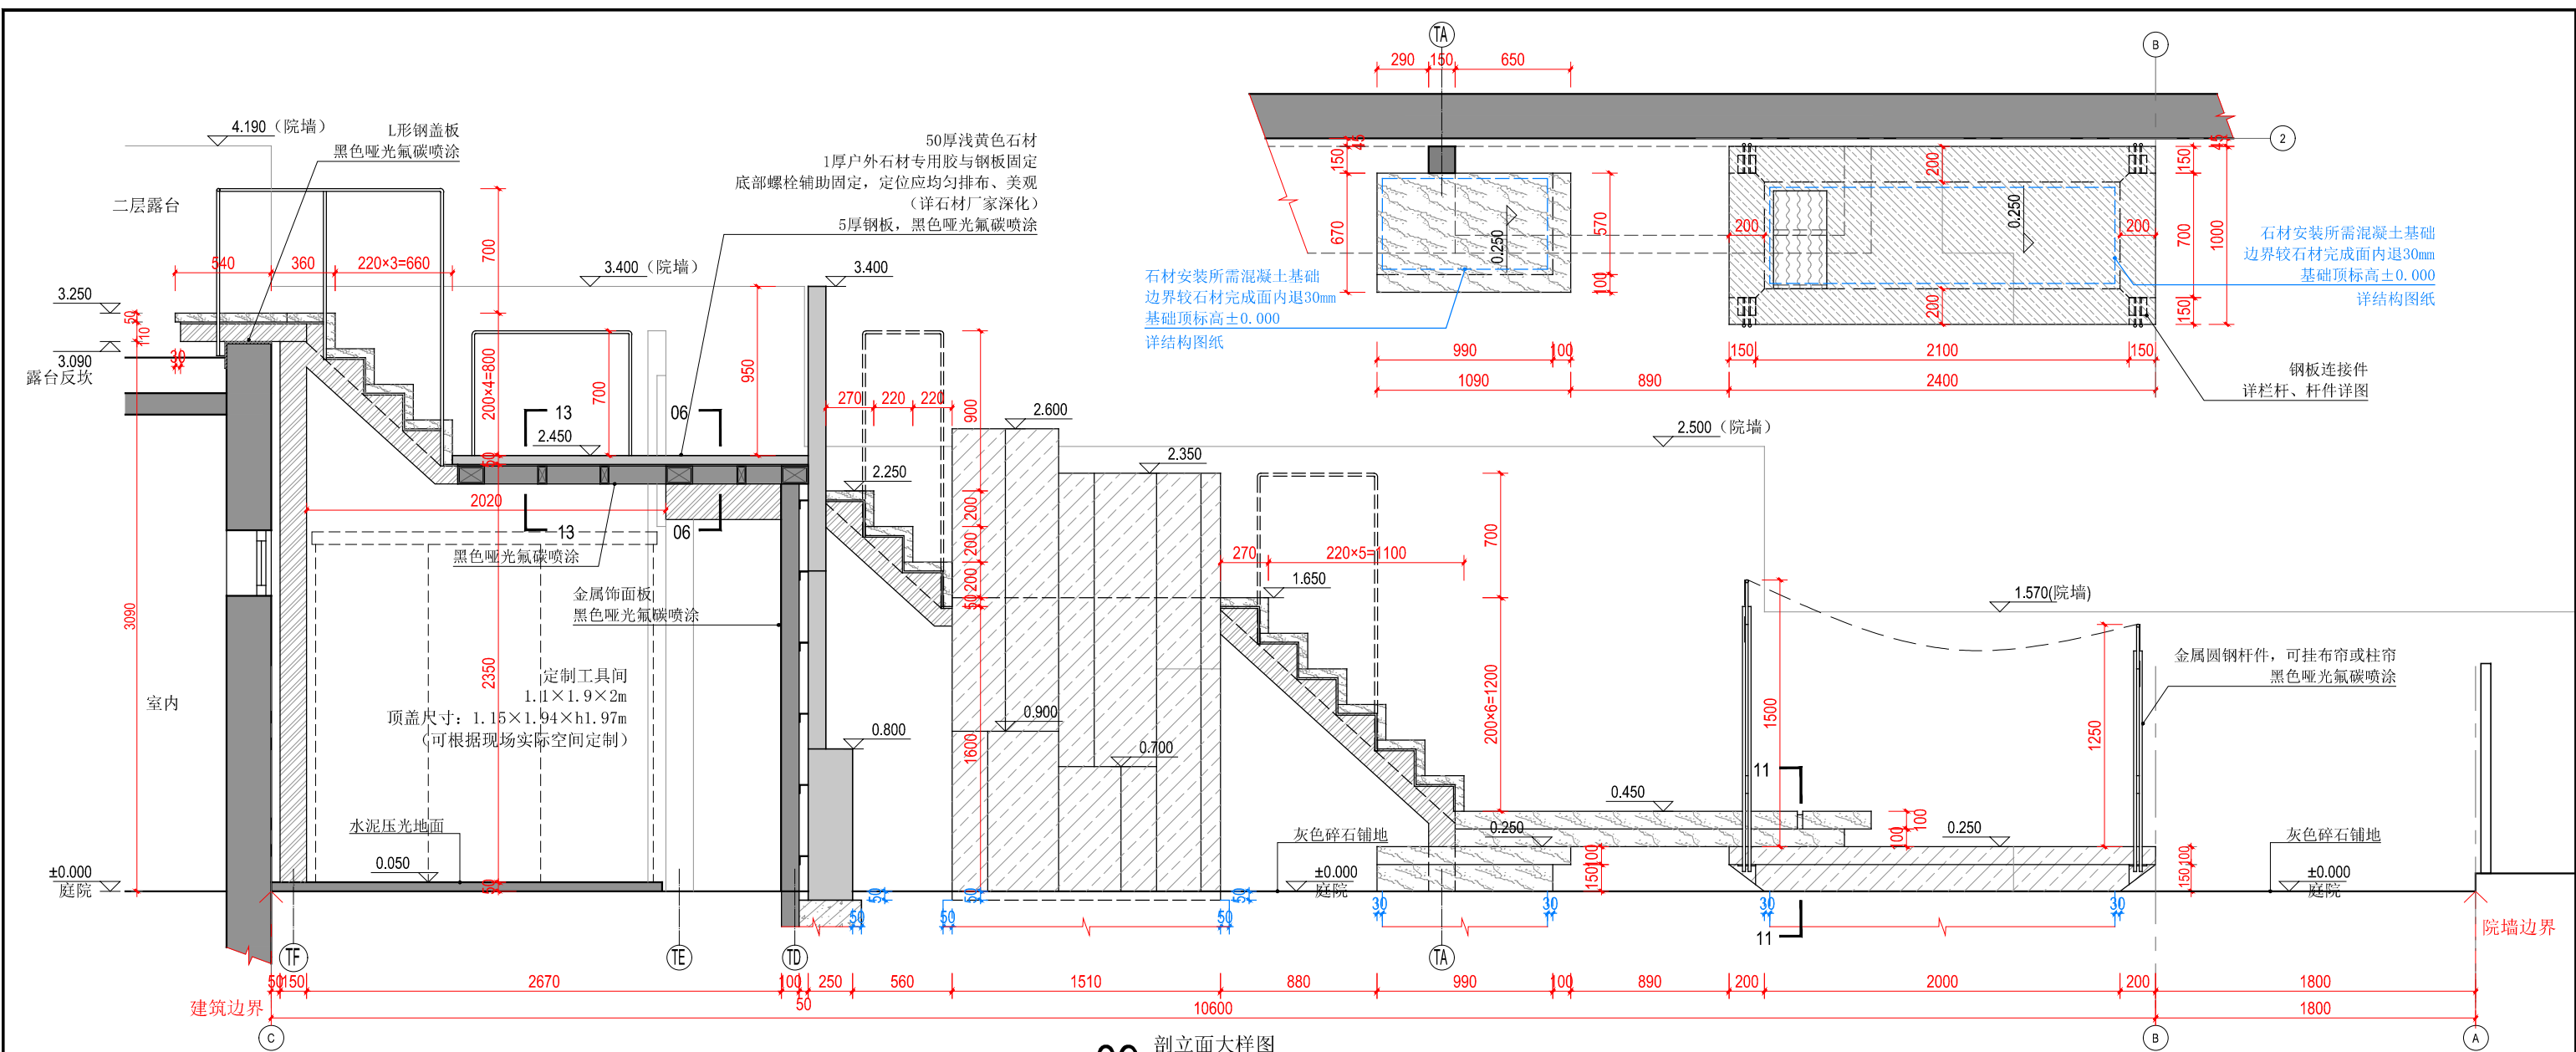


09 剖面大样图
1:20

- 黄色石材
- 浅黄色石材
- 石材剖切面
- 钢结构剖切面(黑色哑光氟碳喷涂)
- 钢结构或金属饰面板
黑色哑光氟碳喷涂
- 金属冲孔板
黑色哑光氟碳喷涂
- 圆钢栏杆/杆件(详栏杆、杆件详图)
黑色哑光氟碳喷涂

注：1、施工前须依据图纸现场放线，复核实际尺寸；如有误差，须反馈至庭院装置设计方复核确认。
2、水井、地下管线位置及埋深以现场实际为准；开挖后向设计方反馈其具体位置、埋深，根据现场实际情况与施工实际经验共同商定处理方式，确认无问题后再施工。
3、石材具体安装方式由石材厂家深化确定。
4、石材尺度、强度及受力性能须满足楼梯平台承载力要求，并经厂家确认无误后方可加工。
如需调整，请反馈至庭院装置设计方复核。

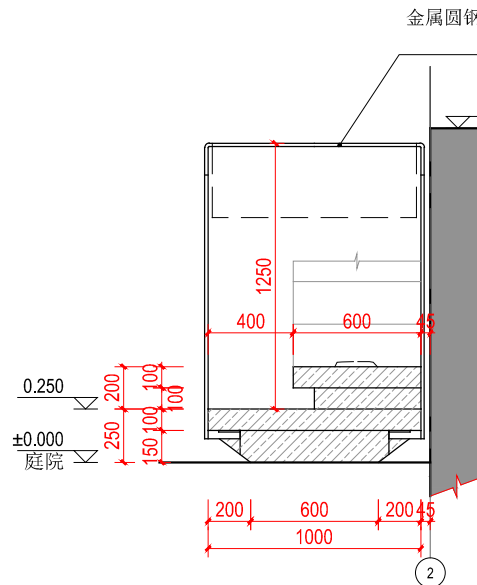


10 剖面大样图
1:20

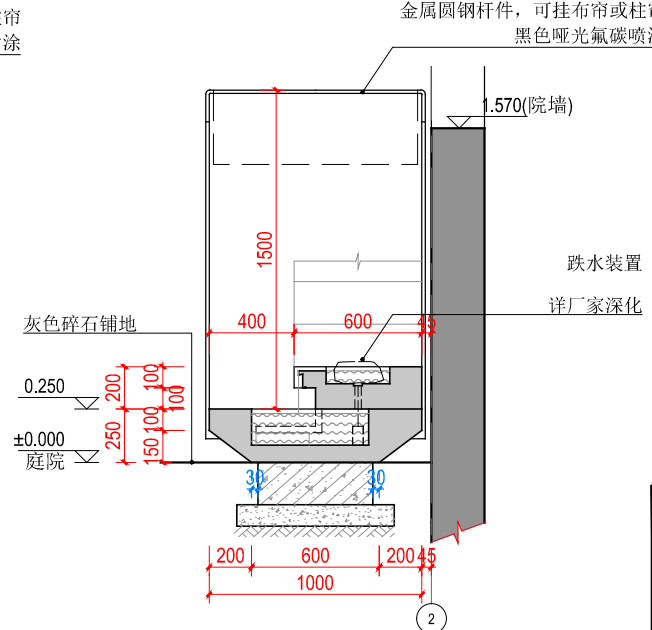


11 剖面大样图
1:20


图别	图名	制图	设计	校对	专业负责人	项目负责人	审核	委托单位	修改版本
A-2.1	建施 剖面大样图(三)							金山岭庭院装置 阿那亚·金山岭	
比例	A2 1:25								
日期	2026年07月								

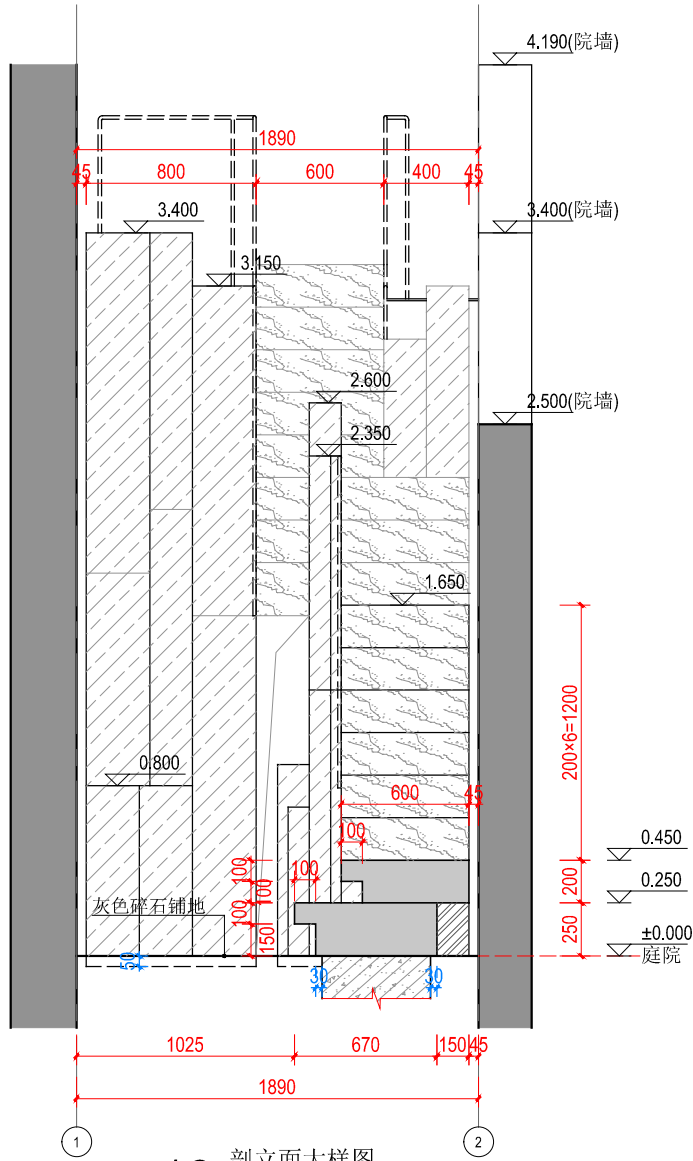

12 剖面大样图
1:20

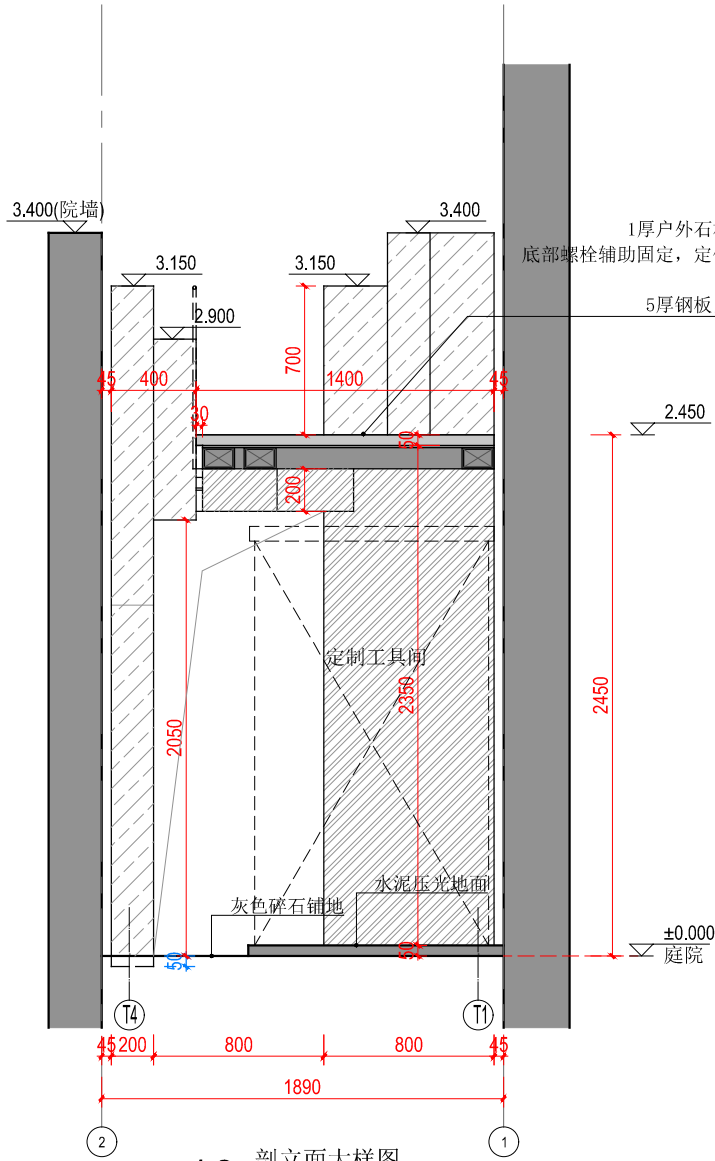


13 剖面大样图
1:20

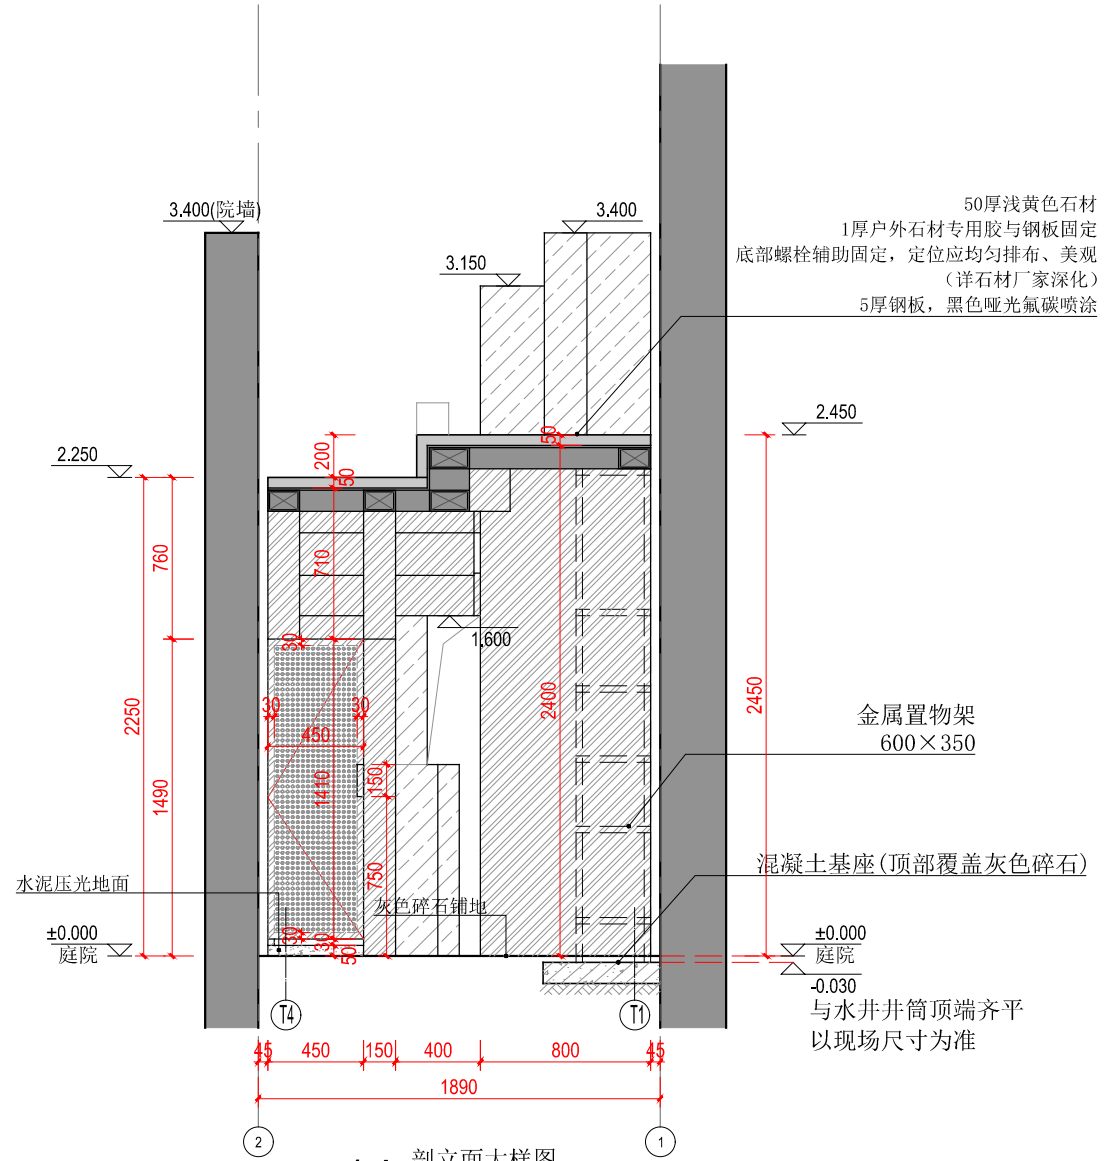

14 剖面大样图
1:20

- 黄色石材
- 浅黄色石材
- 石材剖切面
- 钢结构剖切面(黑色哑光氟碳喷涂)
- 钢结构或金属饰面板
黑色哑光氟碳喷涂
- 金属冲孔板
黑色哑光氟碳喷涂
- 圆钢栏杆/杆件(详栏杆、杆件详图)
黑色哑光氟碳喷涂

注: 1、施工前须依据图纸现场放线, 复核实际尺寸; 如有误差, 须反馈至庭院装置设计方复核确认。
2、水井、地下管线位置及埋深以现场实际为准; 开挖后向设计方反馈其具体位置、埋深, 根据现场实际情况与施工实际经验共同商定处理方式, 确认无问题后再施工。
3、石材具体安装方式由石材厂家深化确定。
4、石材尺度、强度及受力性能须满足楼梯平台承载力要求, 并经厂家确认无误后方可加工。
如需调整, 请反馈至庭院装置设计方复核。

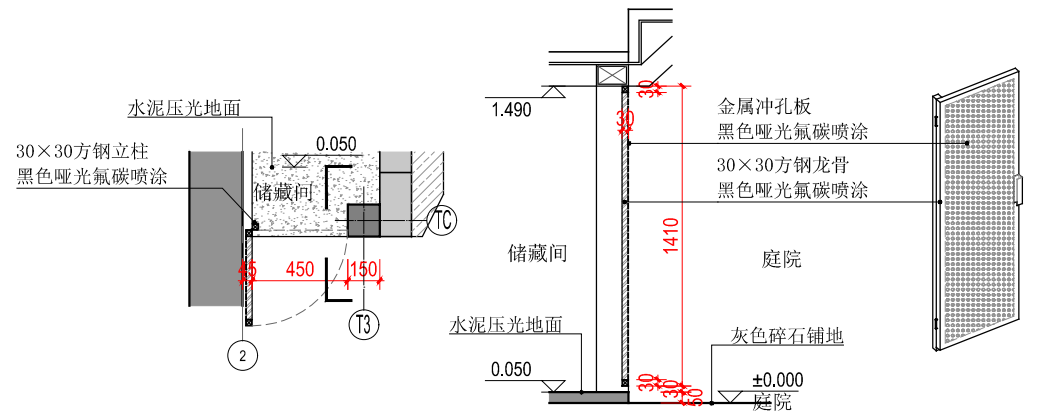

修改版本	
委托单位	金山岭庭院装置
项目编号	阿那亚·金山岭
项目名称	
项目地点	
审核	
项目负责入	
专业负责入	
校对	
设计	
制图	
图别	建造
图名	A-2.1 剖面大样图(四)
比例	A2 1:25
日期	2026年07月

图纸目录

[illegible]

修改版本

委托单位
项目编号
项目名称 金山岭庭院装置
项目地点 阿那亚 金山岭

审核

项目负责人


专业负责人

校对

设计


制图

图别 结施
图名 S-101 基础平面图
比例 1:25
日期 2026年07月

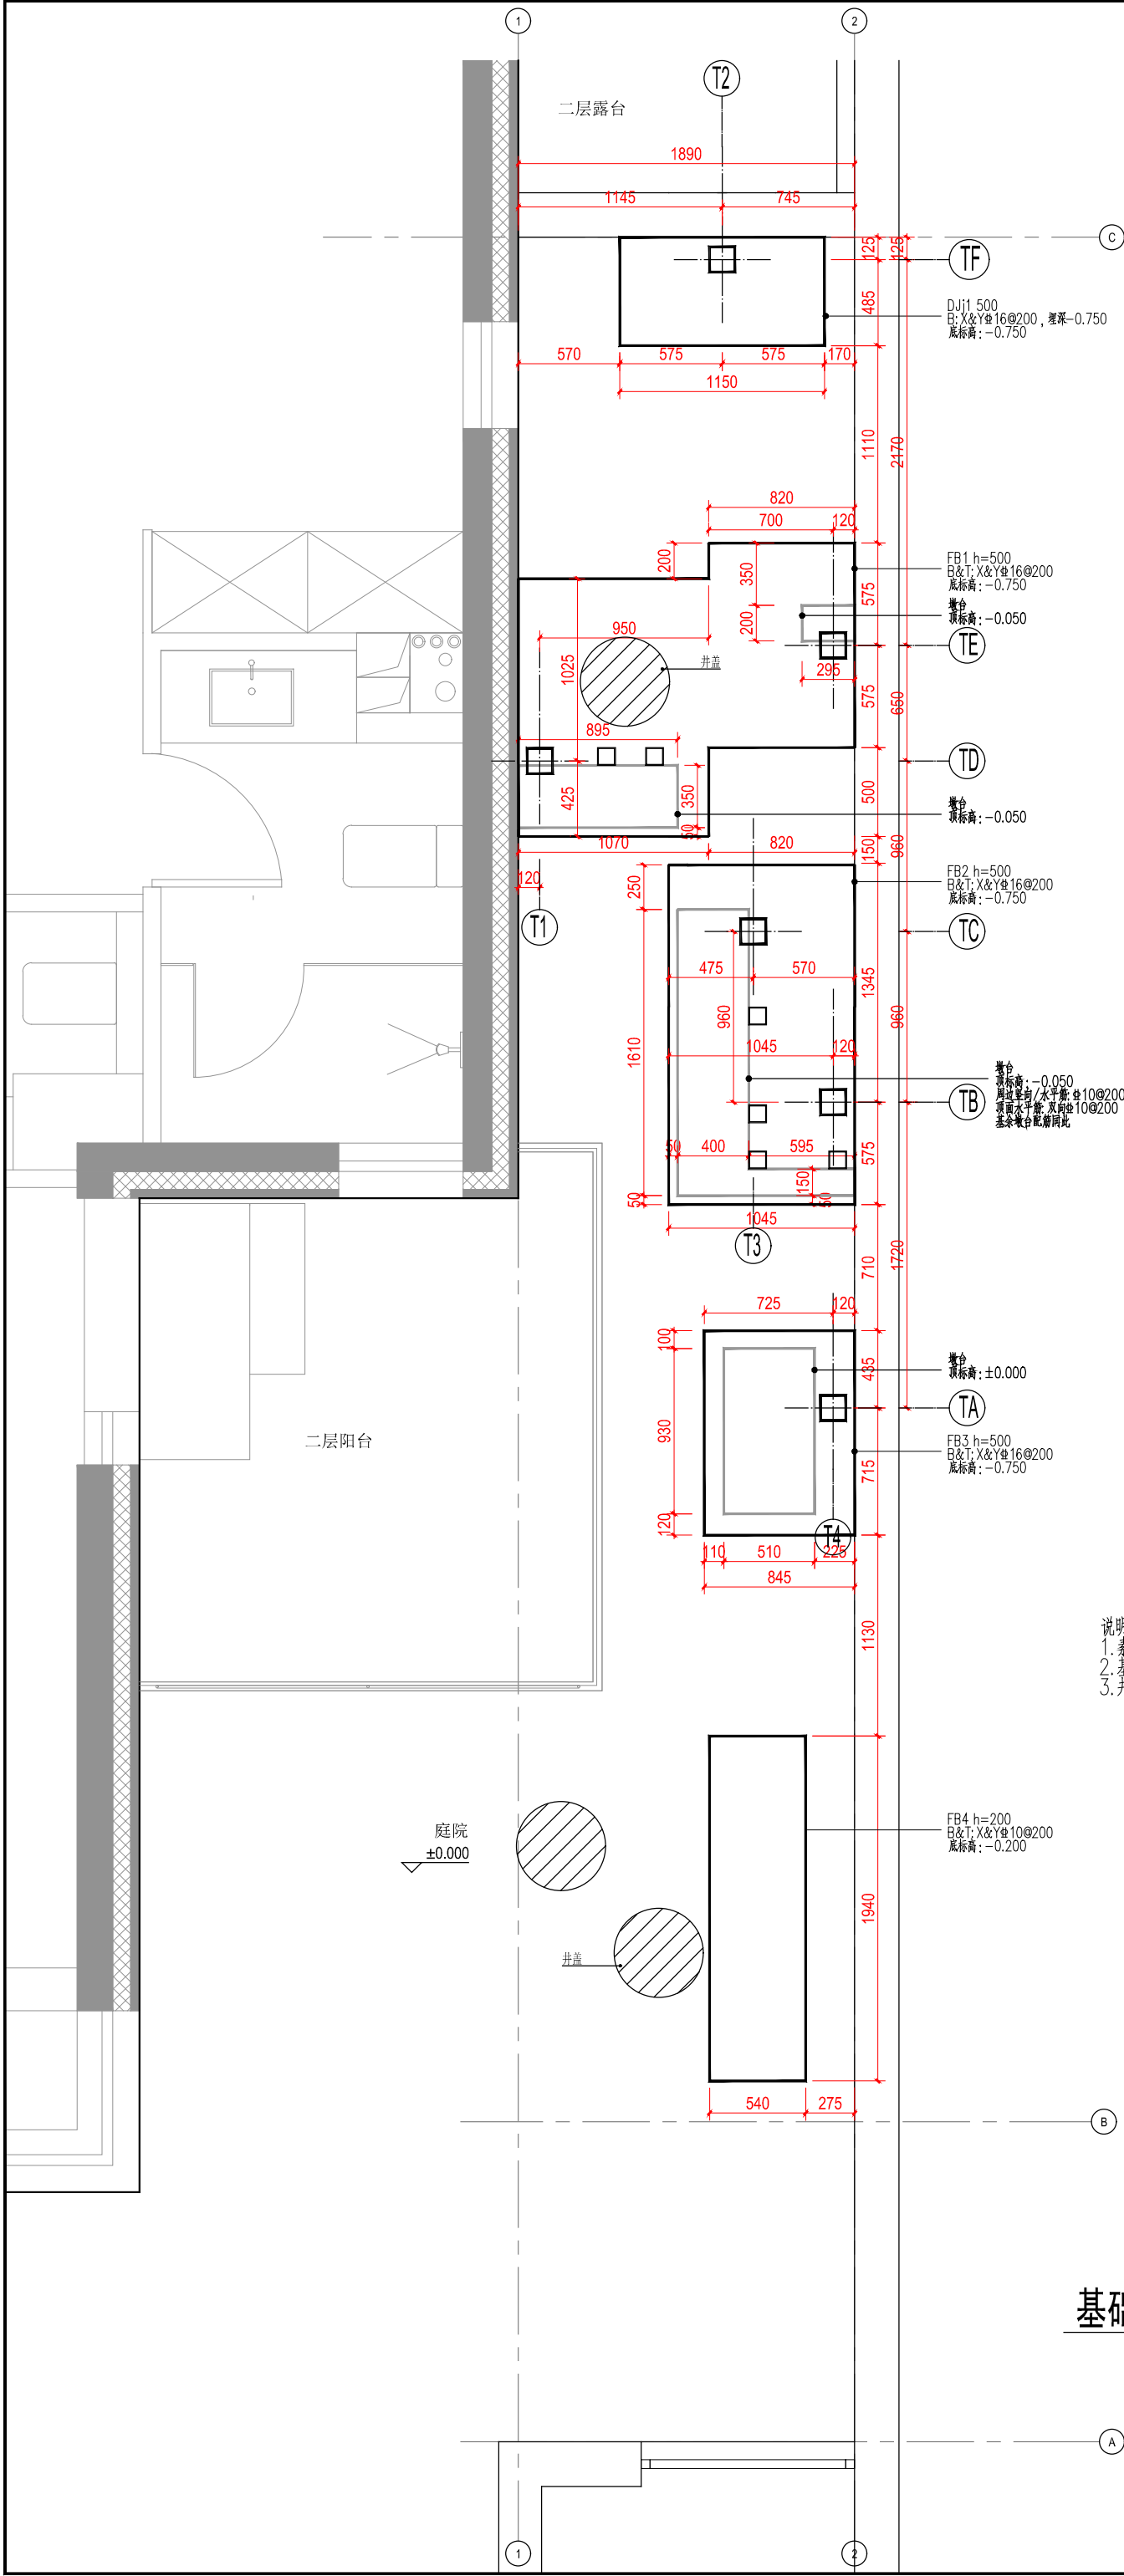

说明:
1.素混凝土垫层强度等级C15,厚度100;
2.基础混凝土强度等级C35;
3.井盖和地下管线位置、埋深以现场实际为准,开挖后向设计单位反馈其具体位置、埋深,确认无问题后再施工。

基础平面图
1:25

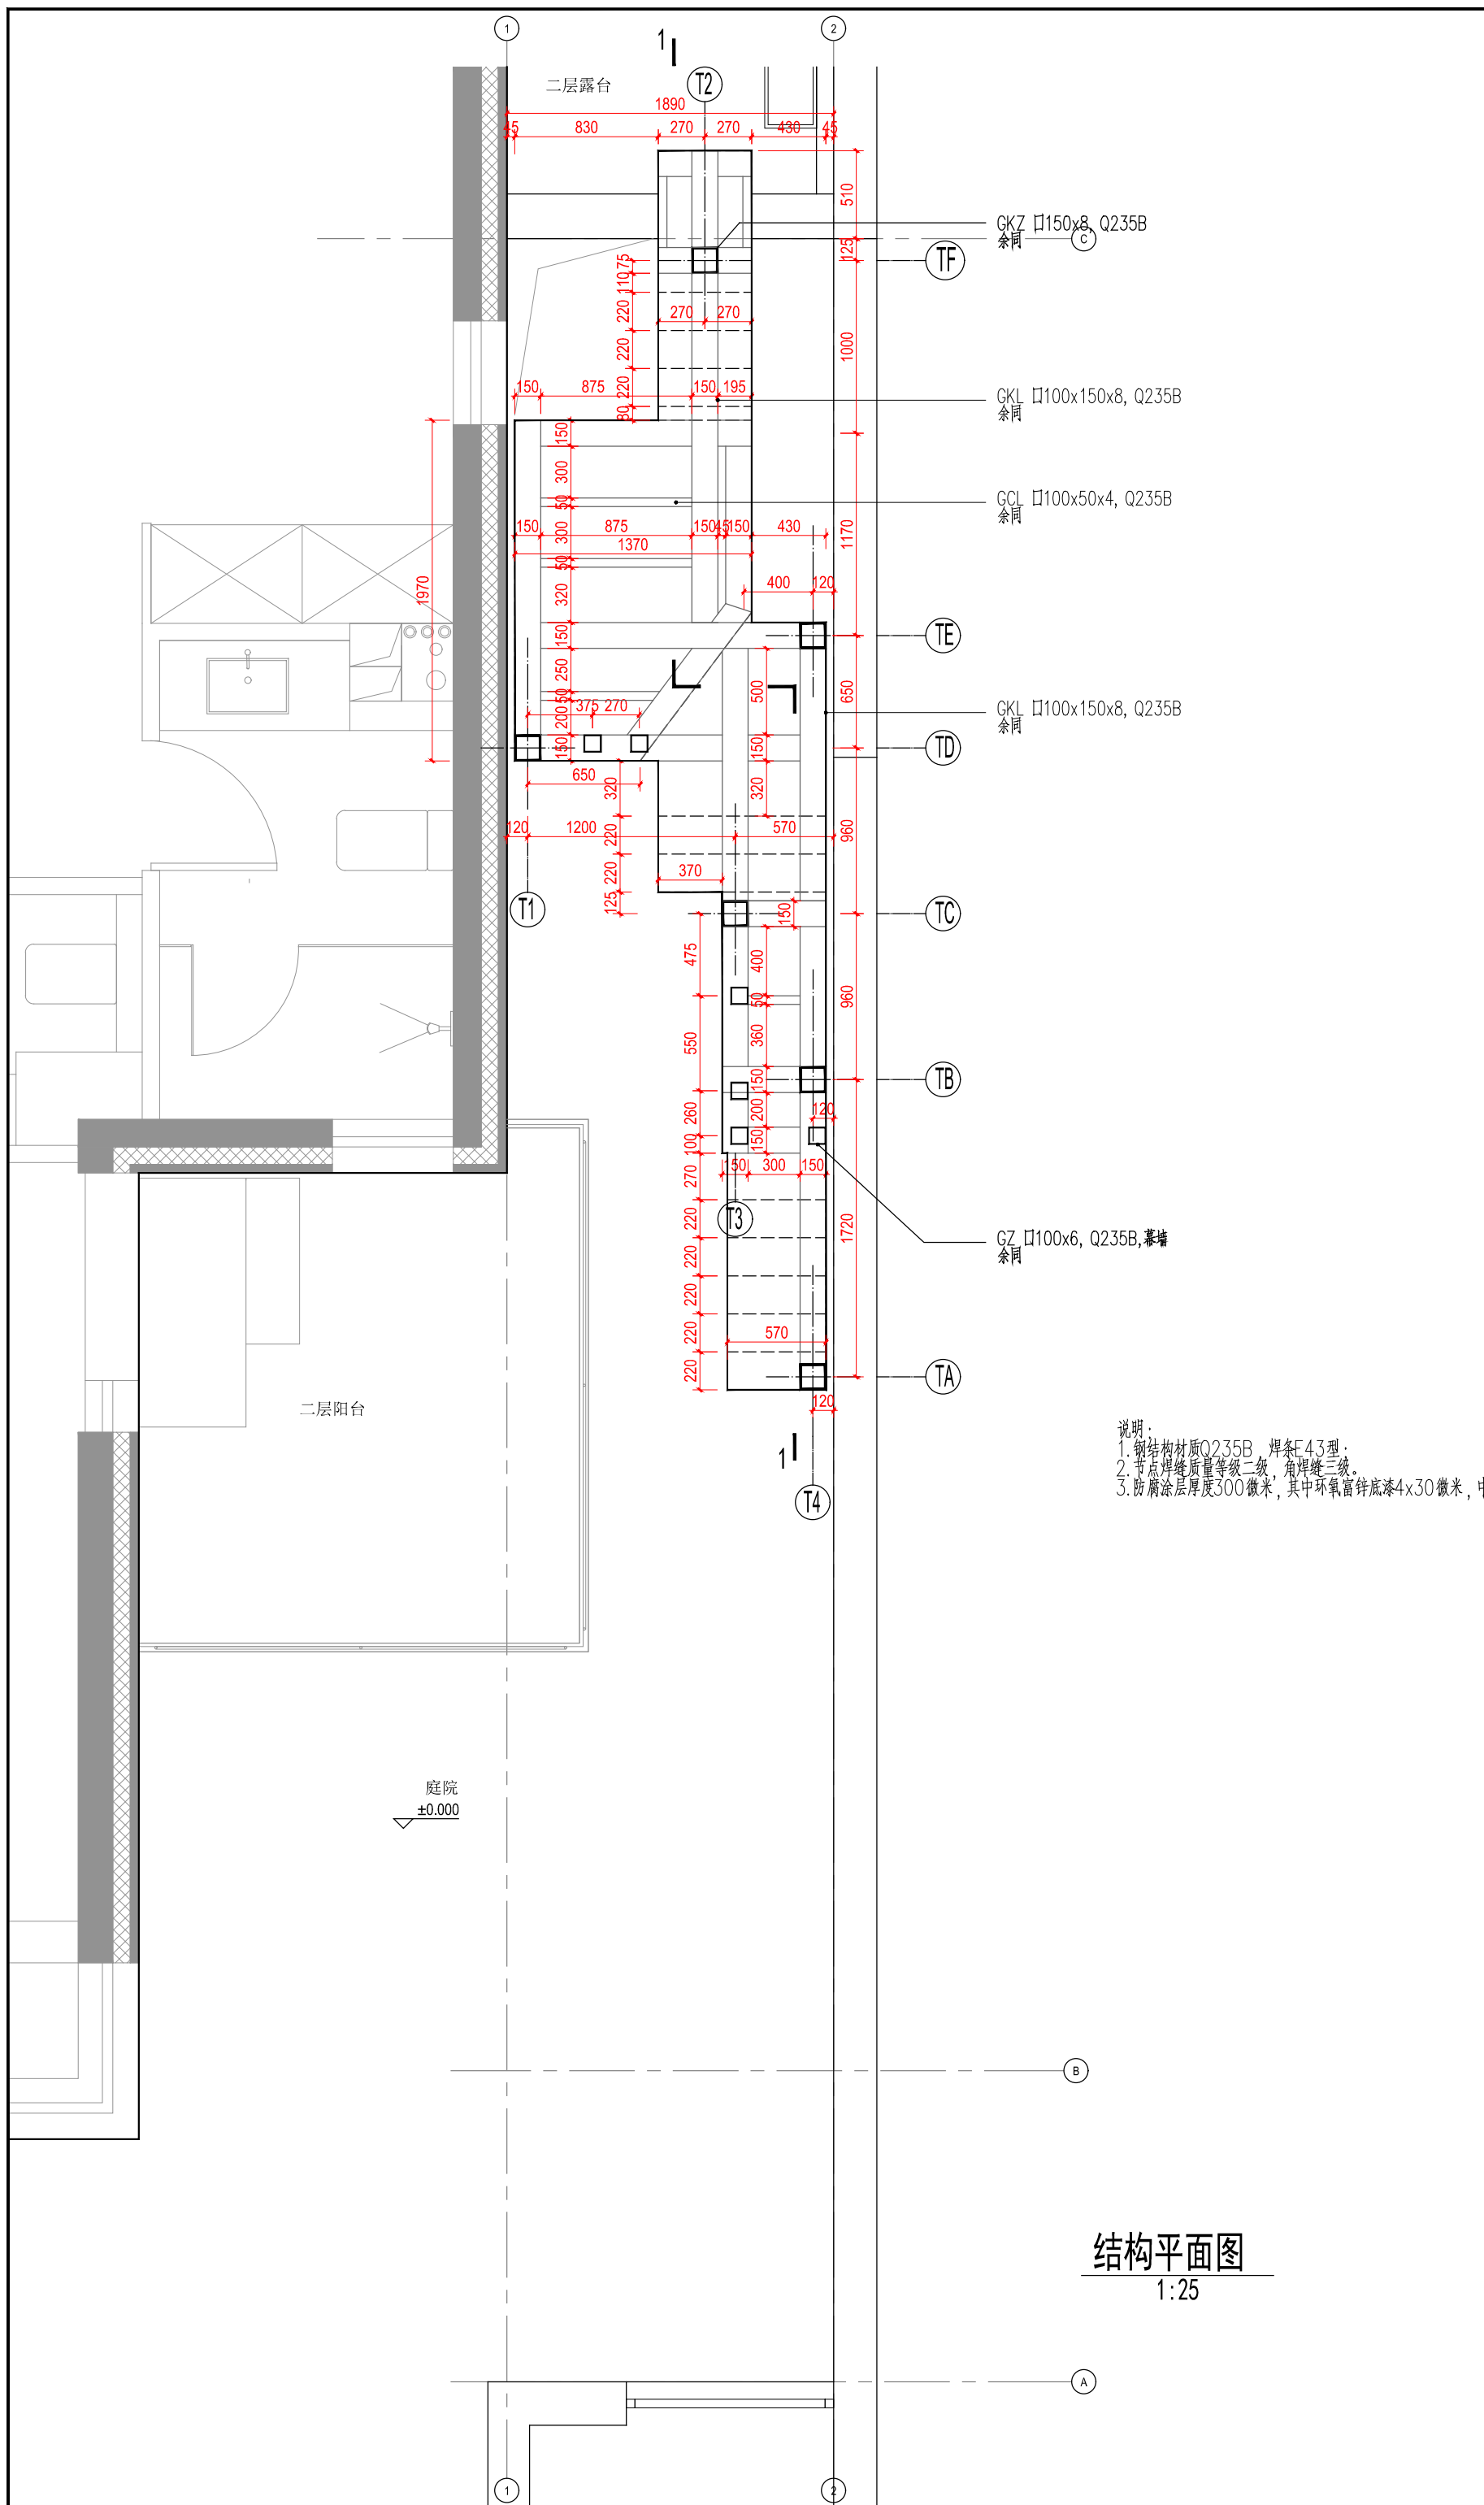

修改版本

委托单位	
项目编号	
项目名称	金山岭庭院装置
项目地点	阿那亚 金山岭

审核

项目负责人


专业负责人

校对

设计

制图


图别	结施
图名 S-201	结构平面图
比例	1:25
日期	2026年07月

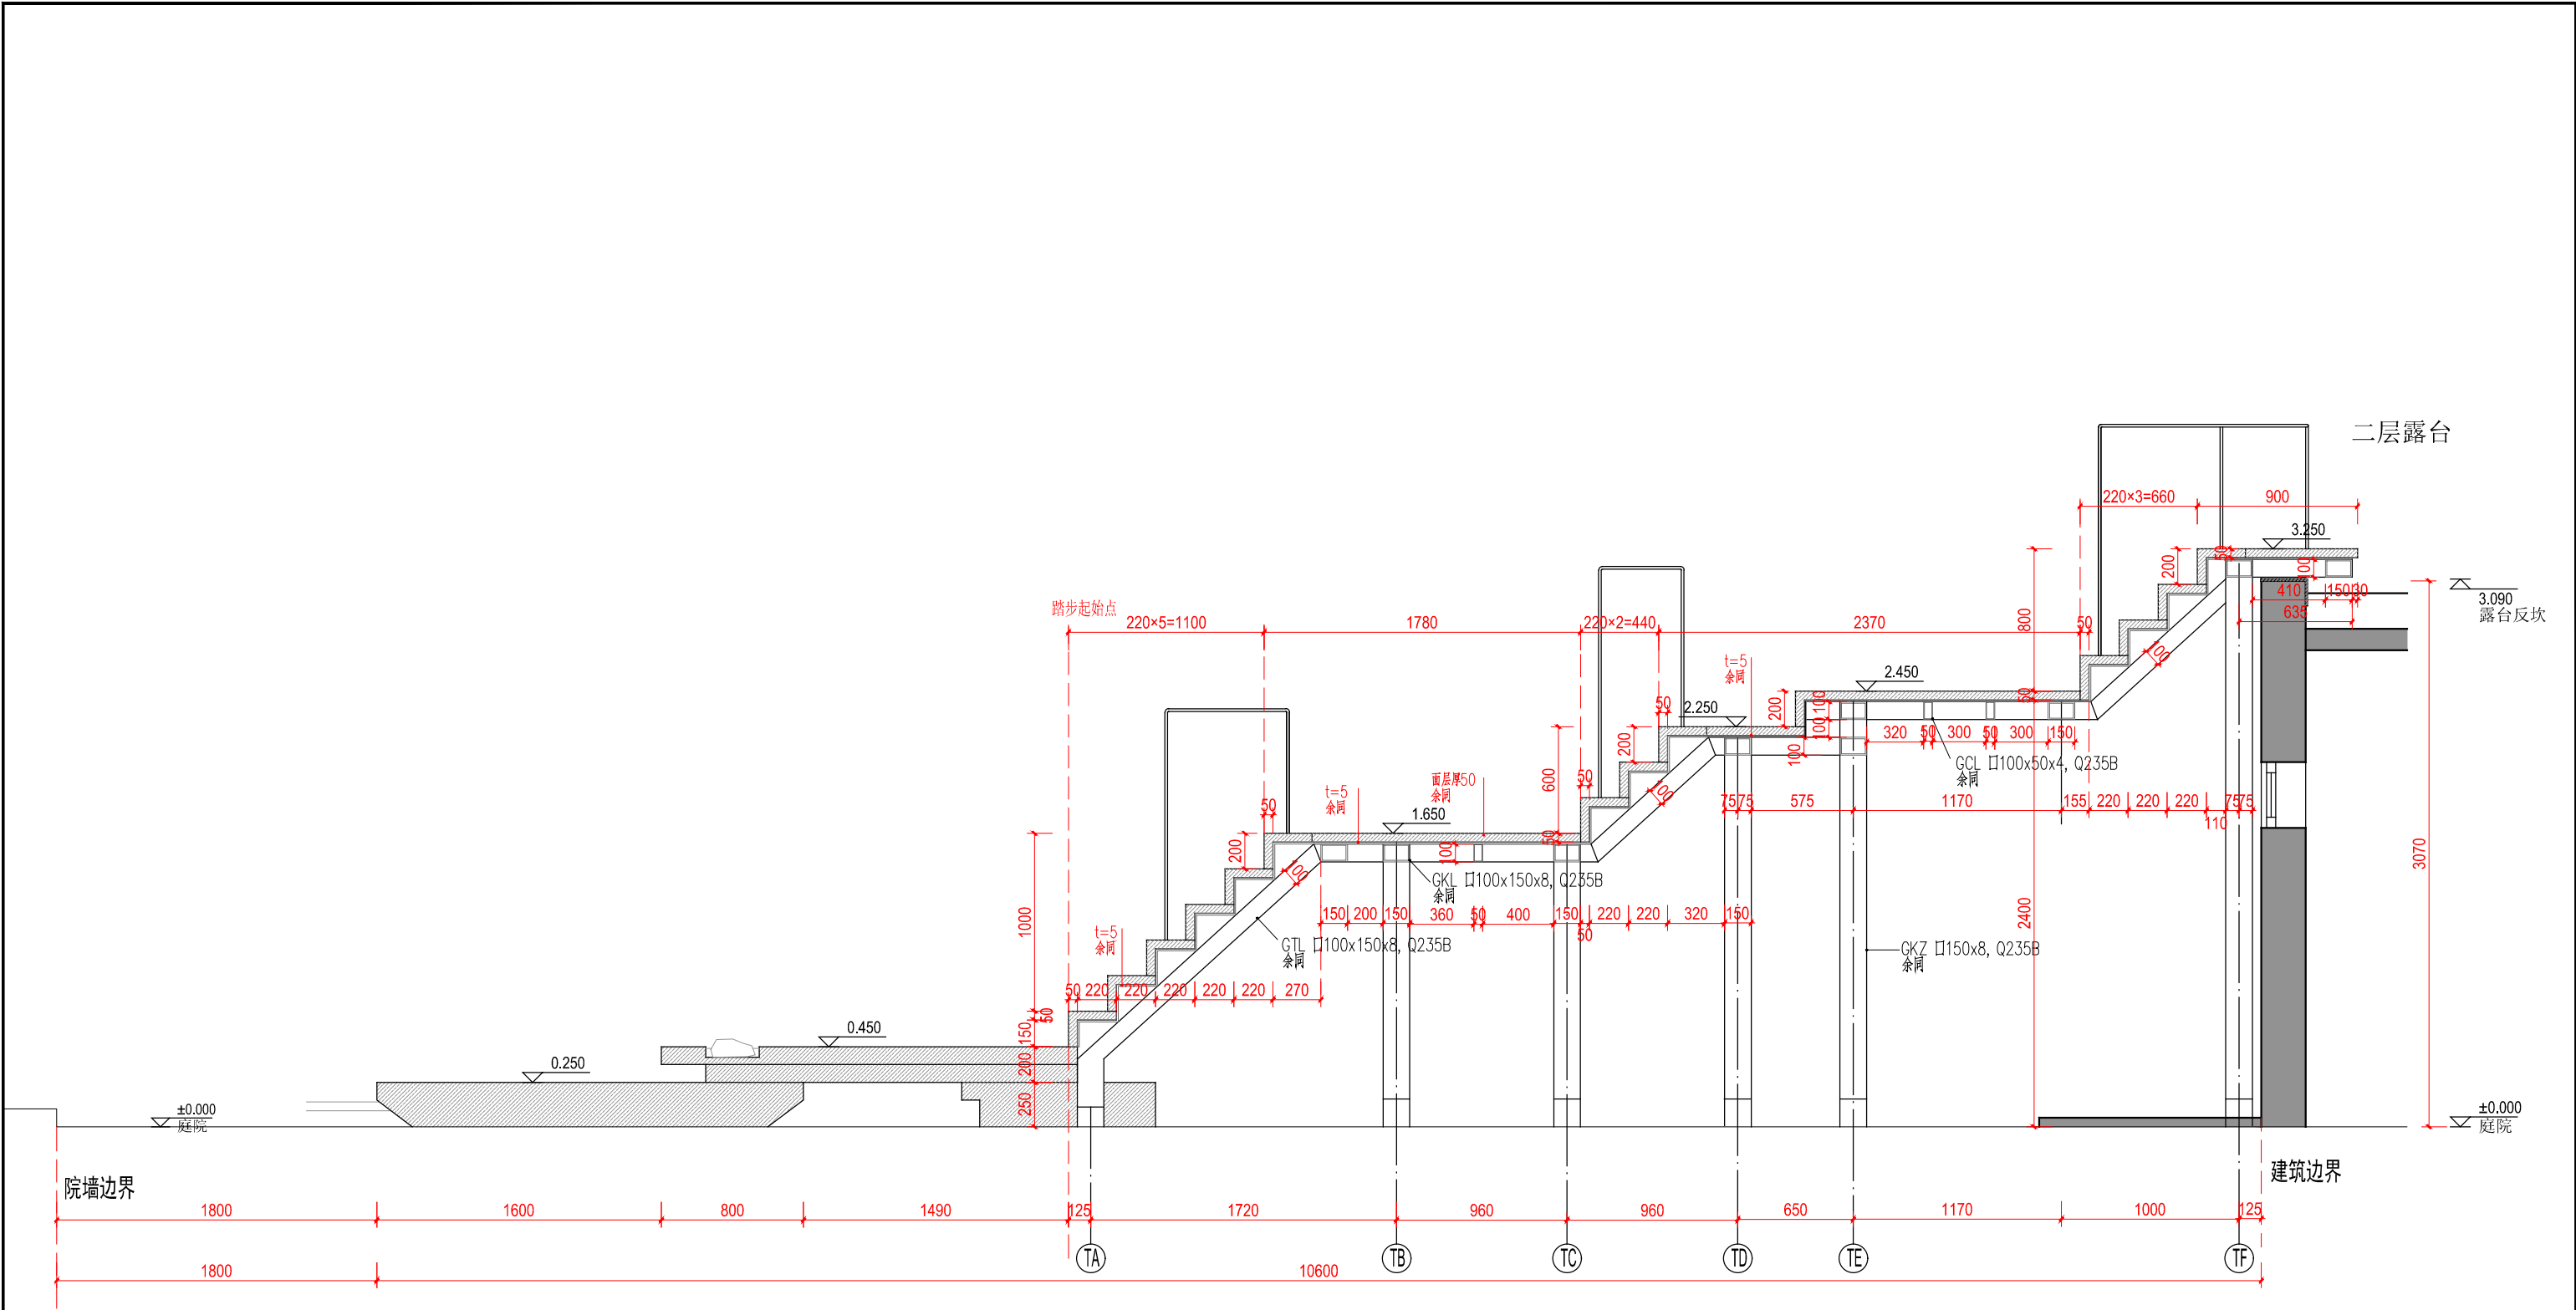


1-1剖面详图

1:25


修改版本	
委托单位	金山岭庭院装置
项目编号	阿那亚·金山岭
项目名称	
项目地点	
审核	
项目负责人	
专业负责人	
校对	
设计	
制图	
图别	结施
图名	S-301 剖面详图
比例	1:25
日期	2026年07月

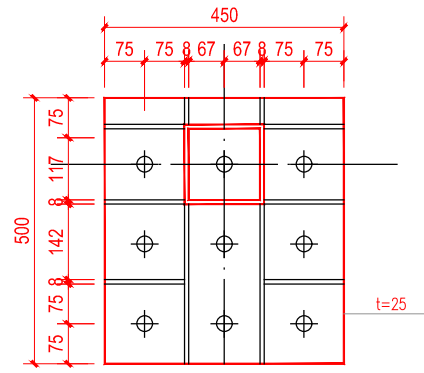


A-A
偏心柱脚

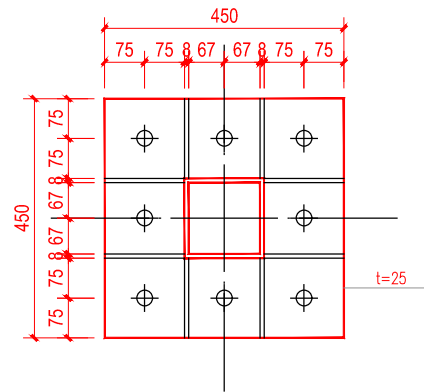


A-A

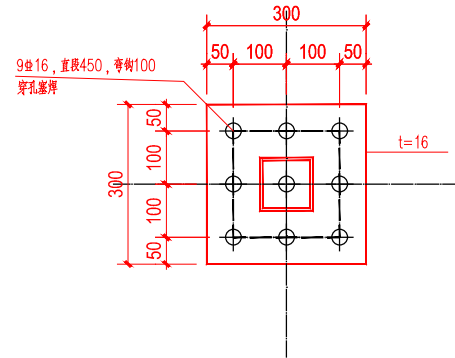


幕墙柱脚埋件

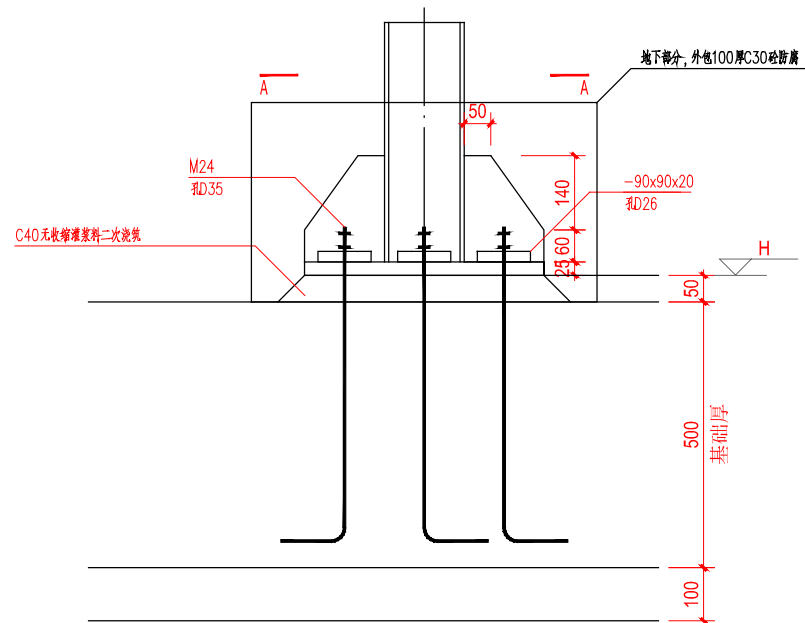


钢柱脚节点 1:10

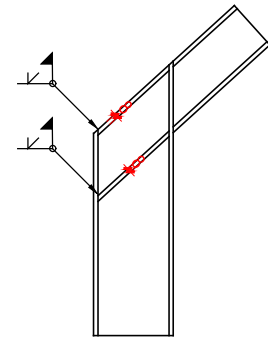


钢梯梁底端节点 1:10

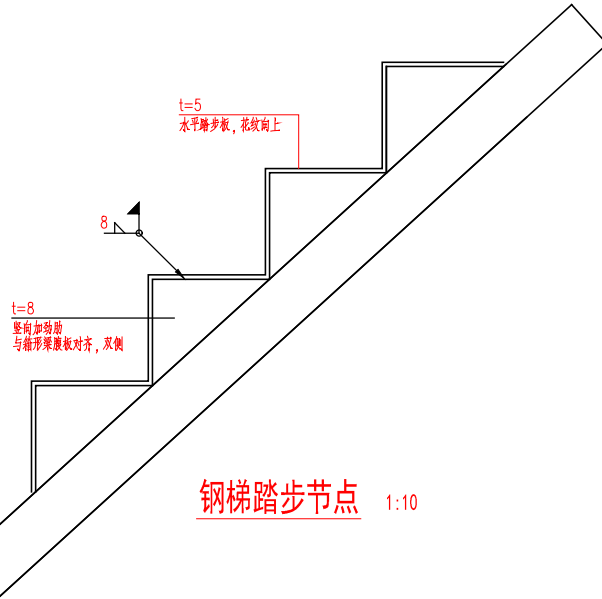

钢梯踏步节点 1:10

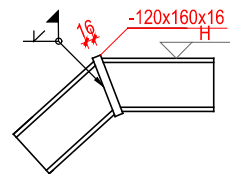

梯梁转折节点 1:10

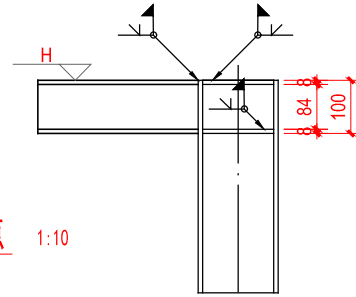

梁柱节点 1:10

修改版本

委托单位

项目编号

项目地点

项目地点 阿那亚 金山岭

项目地点 阿那亚 金山岭

审核

项目负责人

专业负责人

校对

设计

制图



图别


施结

比例 1:10

比例 1:10

日期 2026年07月

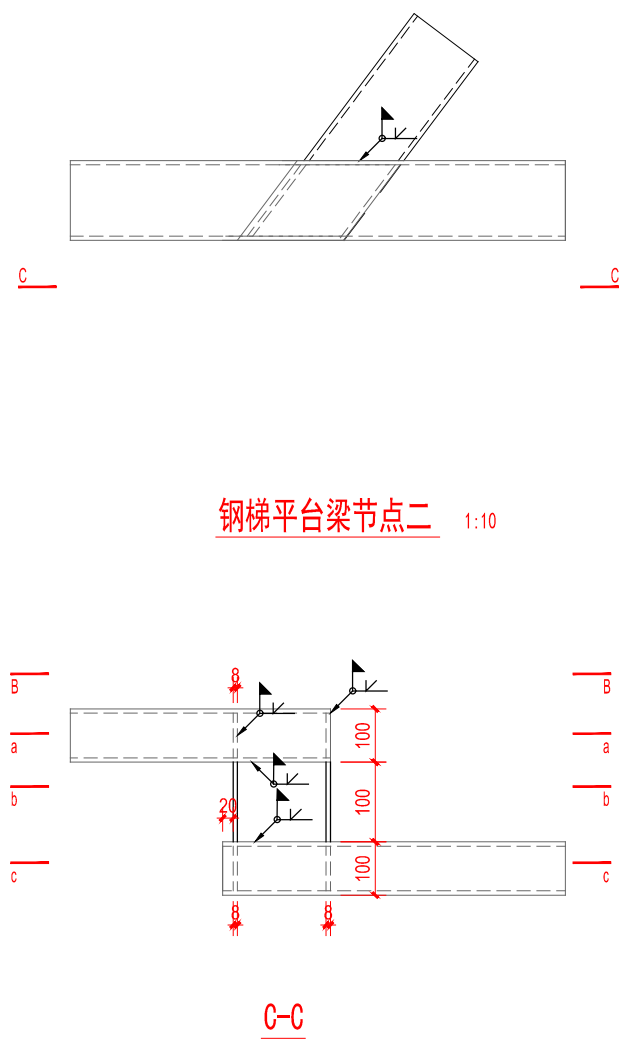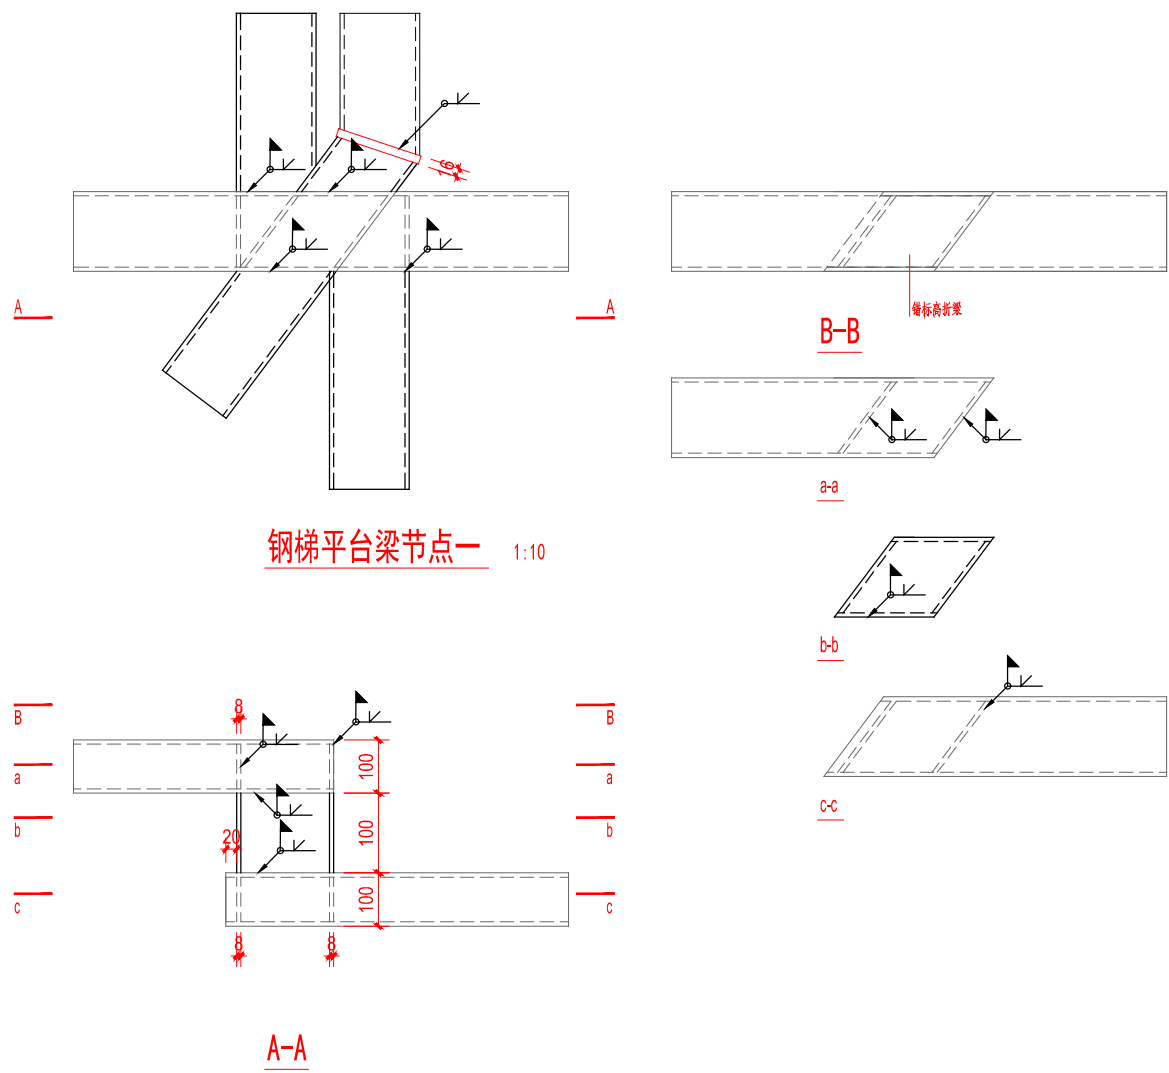

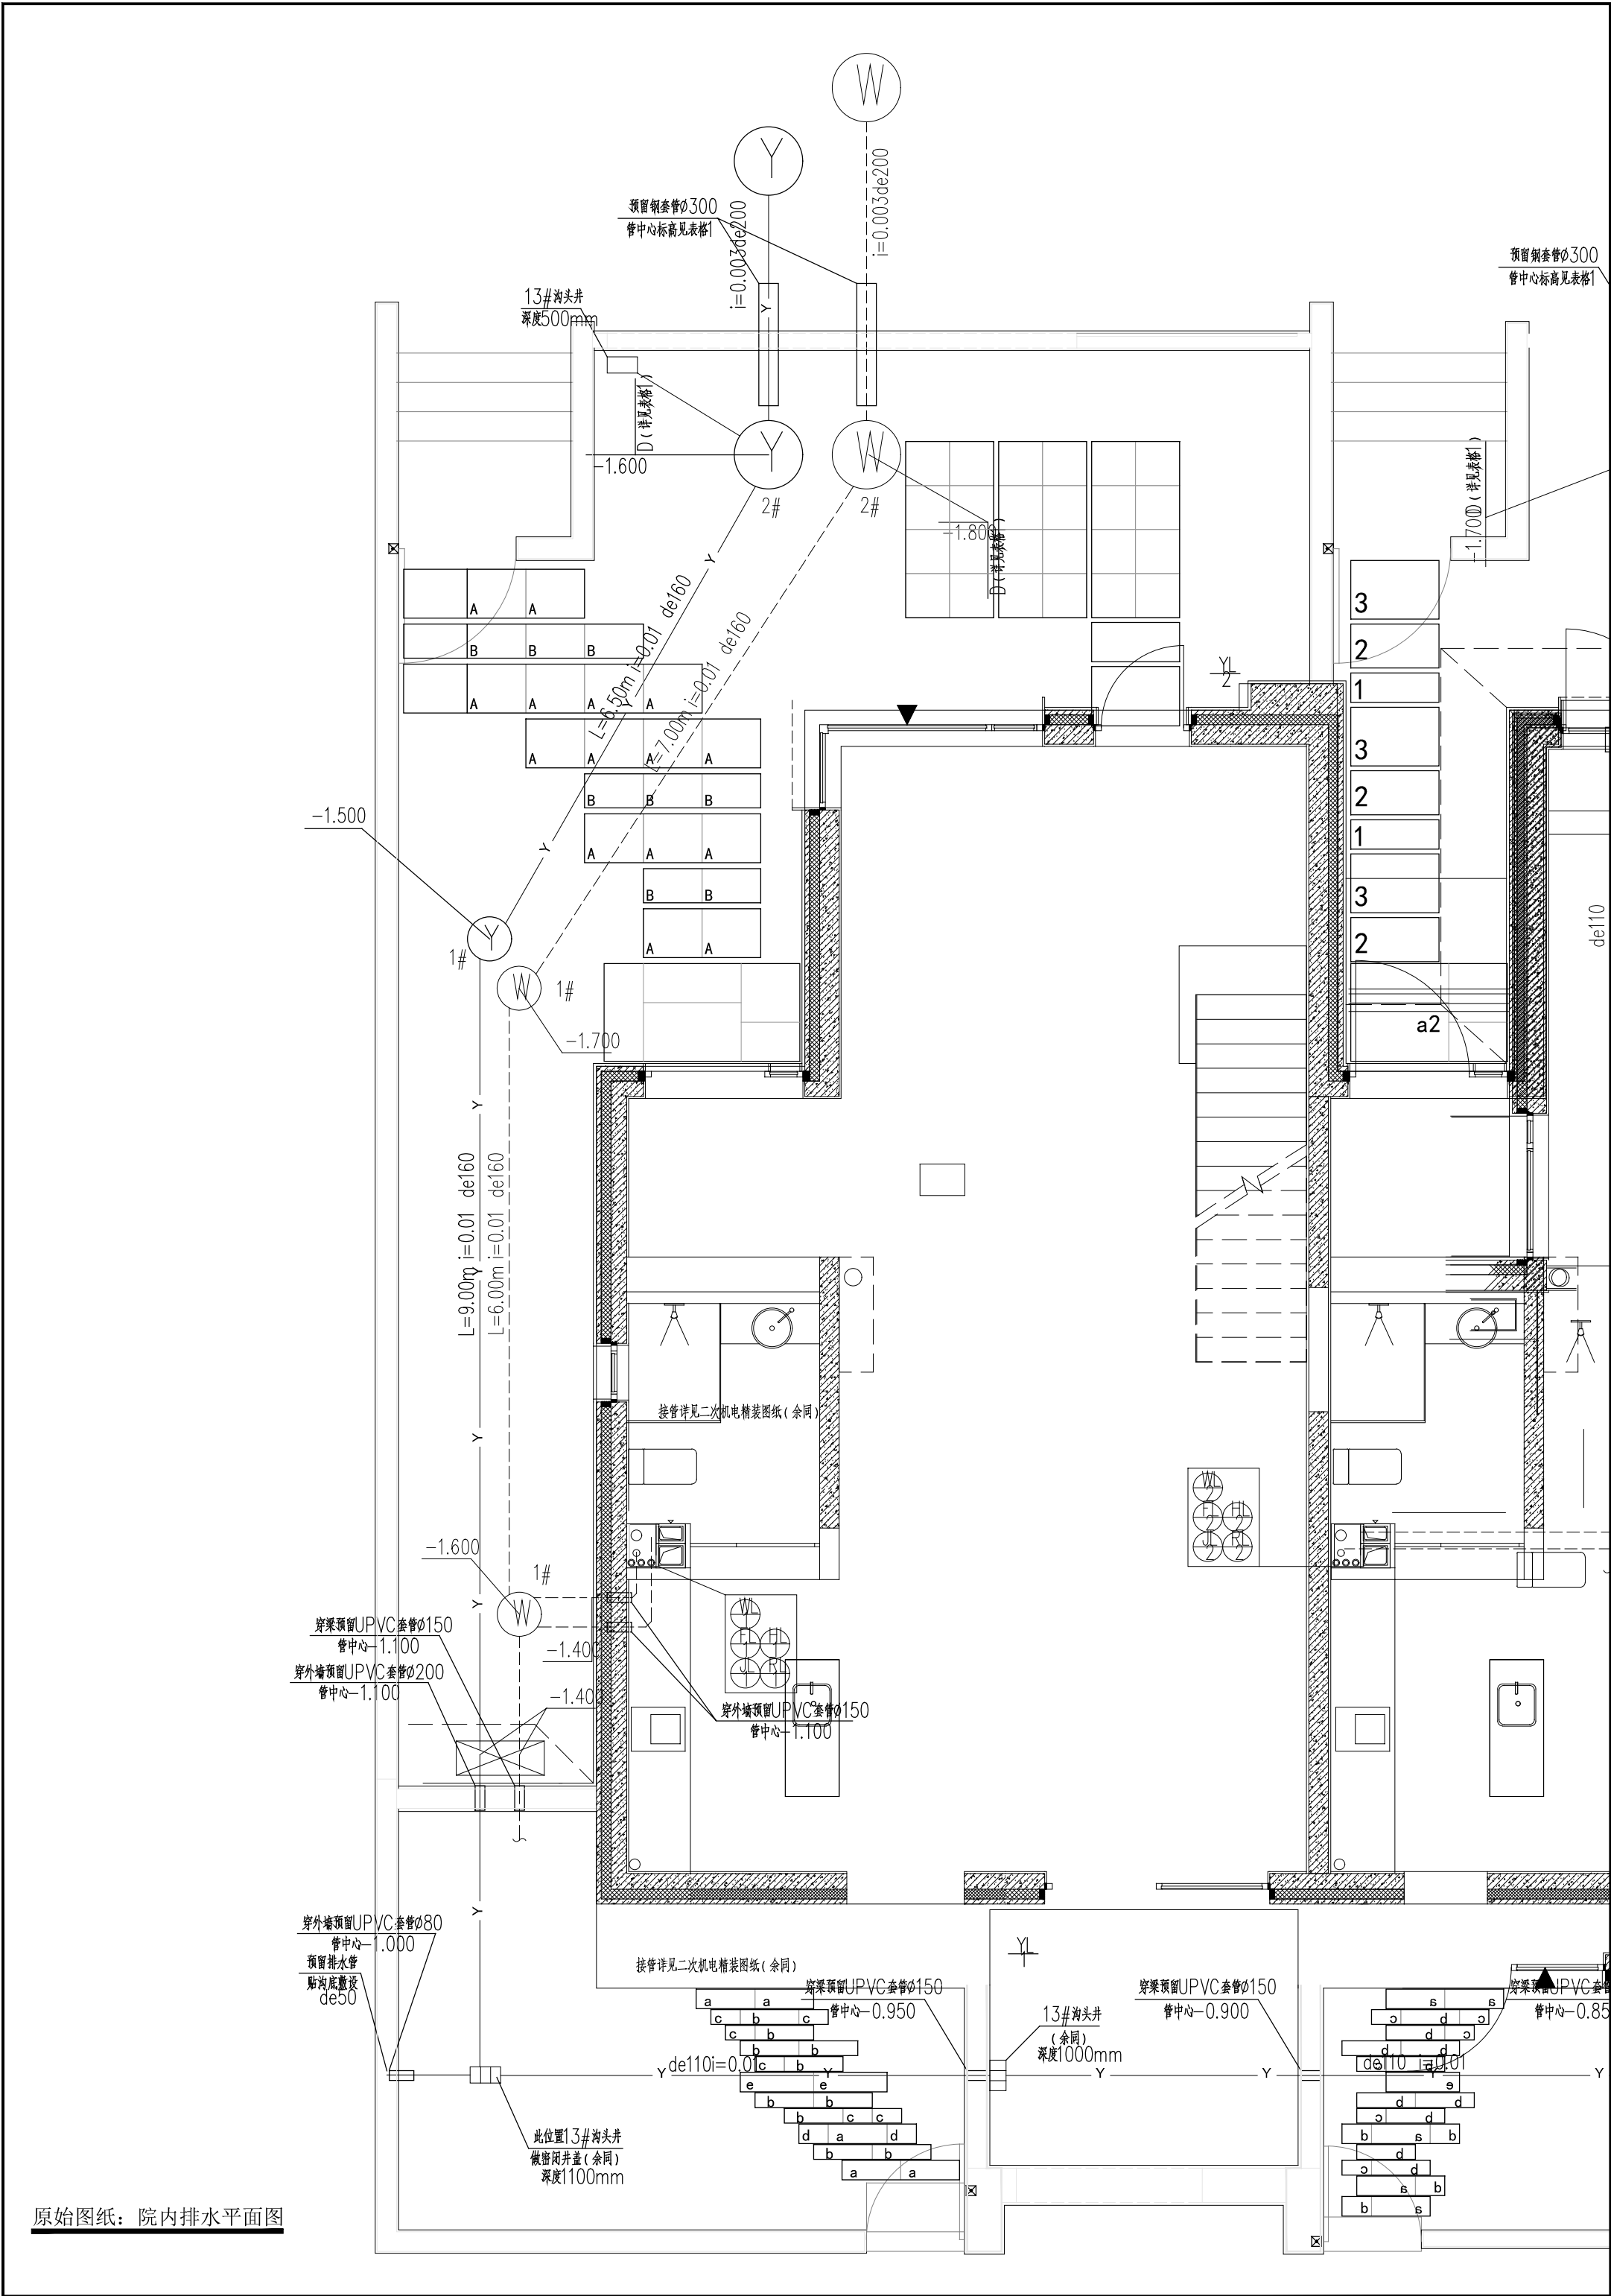

原始图纸：院内排水平面图